
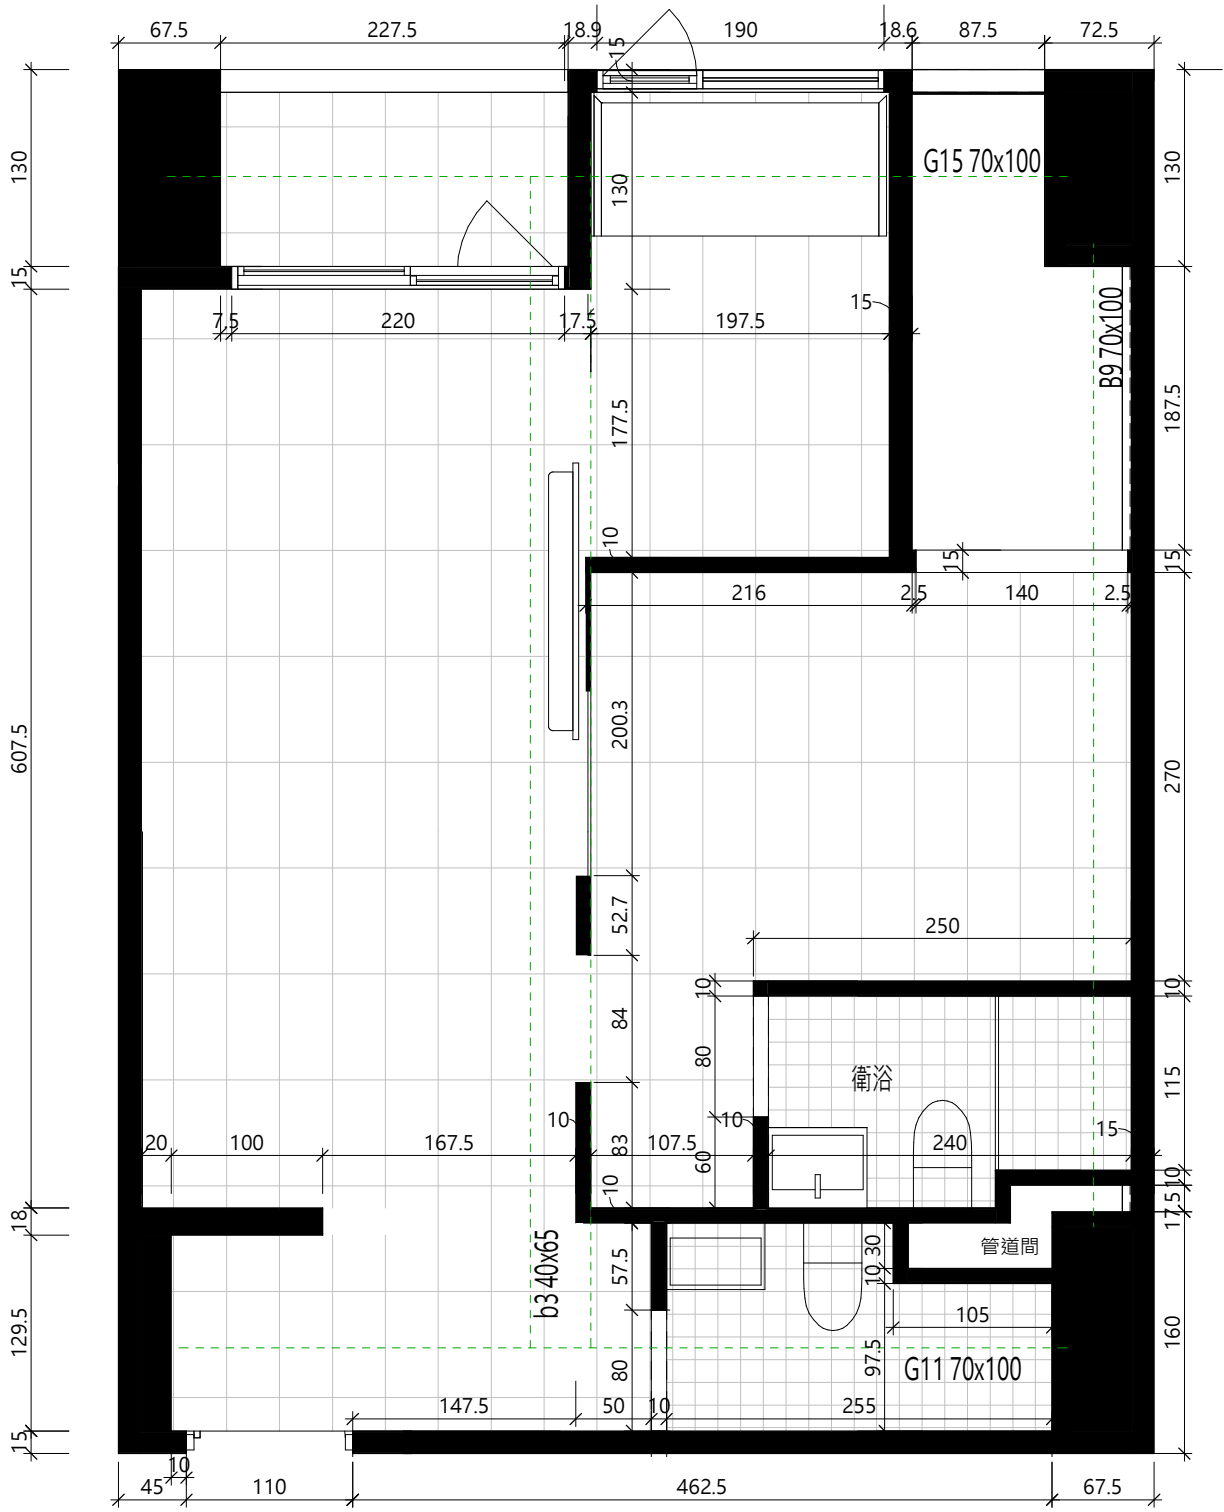


	01	02	03	04	05	06	07	08	09	10	11													
H												客戶/項目名稱： 遠雄建設 BH7接待中心												
												設計方： 												
G												標記/施工方：												
F																								
E																								
D																								
C												提歷： 此圖紙非完全正確比例尺 內存些微誤差。 如發現任何圖紙 及其他文件 具有差異 請立即通知本司顧問。 並在下列情況下 應放棄此圖紙 以修訂版本代替。 本司具有此圖紙版權。												
																								
B												室內設計												
												目錄												
												<table><tr><td>項名</td><td>專案編號</td></tr><tr><td>階段</td><td>專案狀態</td></tr><tr><td>尺寸</td><td>A3</td></tr><tr><td>圖號</td><td>I1A6-00</td></tr><tr><td>比例</td><td></td></tr><tr><td>日期</td><td>02/07/25</td></tr></table>	項名	專案編號	階段	專案狀態	尺寸	A3	圖號	I1A6-00	比例		日期	02/07/25
項名	專案編號																							
階段	專案狀態																							
尺寸	A3																							
圖號	I1A6-00																							
比例																								
日期	02/07/25																							
A																								

A6目錄	
圖紙號碼	圖紙名稱

I1A6-00	目錄
I1A6-01	A6建照圖、隔間尺寸圖
I1A6-02	A6平面圖
I1A6-03	A6立面圖1
I1A6-04	A6立面圖2
I1A6-05	A6立面圖3
I1A6-06	A6天花圖
I1A6-07	A6櫃體圖1
I1A6-08	A6櫃體圖2
I1A6-09	A6櫃體圖3
I1A6-10	A6櫃體圖4
I1A6-11	A6櫃體圖5

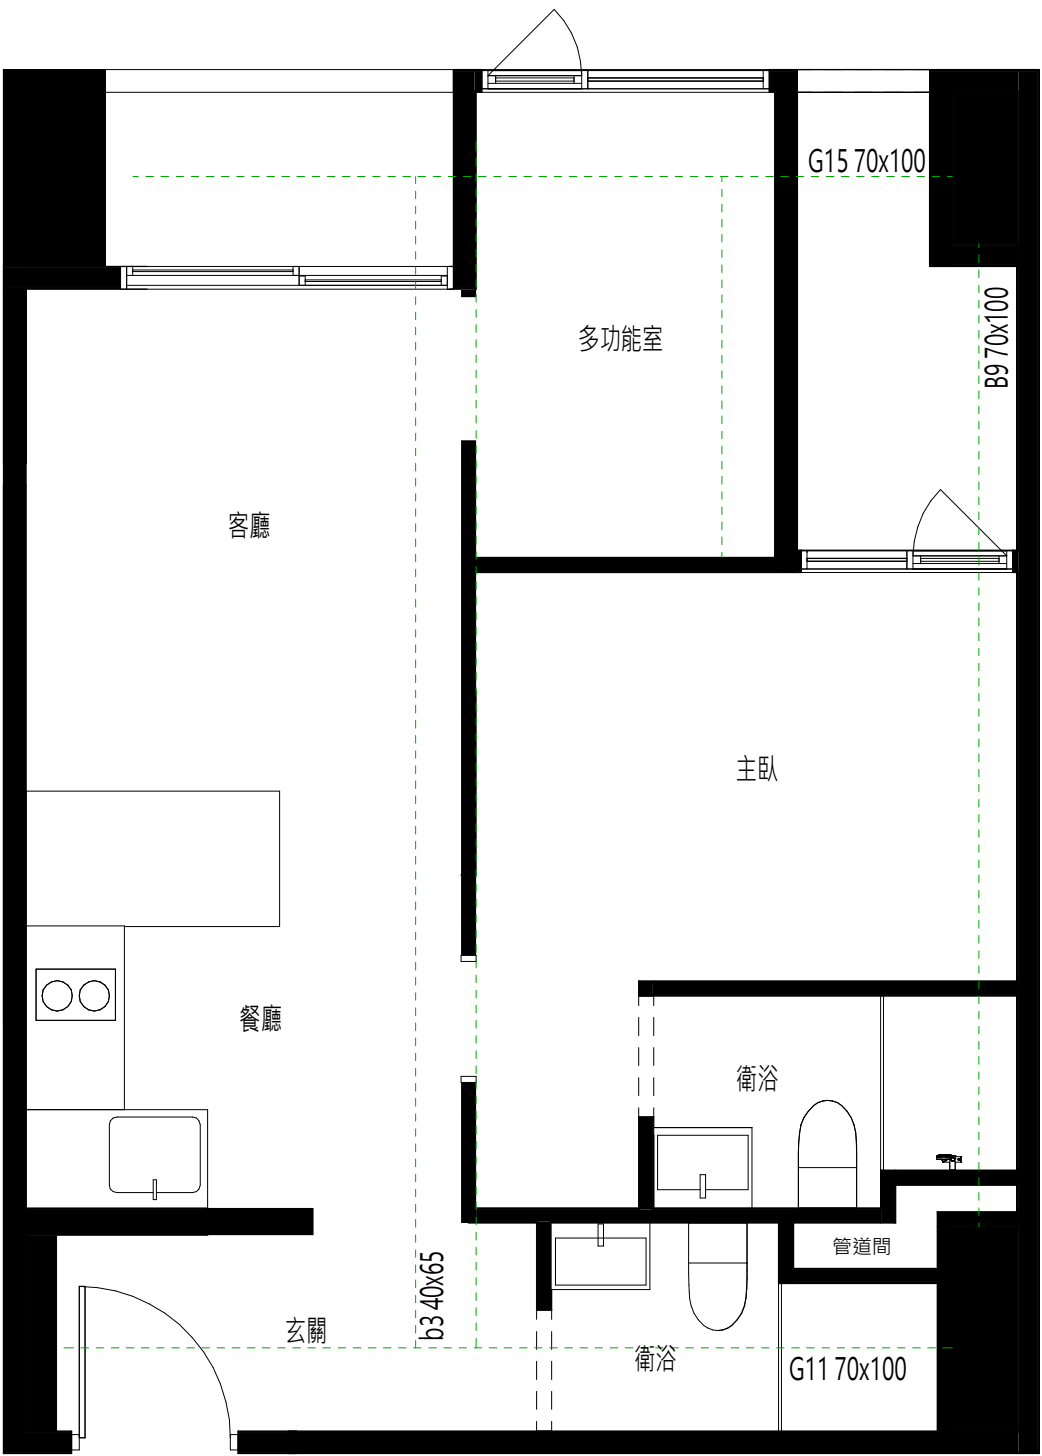

客戶/項目名稱:

遠雄建設
BH7接待中心

設計方:



標記施工方:

提醒:


此圖紙非完全正確比例尺
內存些微誤差
如發現任何圖紙
及其他文件
具有差異
請立即通知本司顧問。
並在下列情況下
應放棄此圖紙
以修訂版本代替。
本司具有此圖紙版權。


參木辛所


室內設計


A6建照圖、隔間尺寸圖

項名	專案編號
階段	專案狀態
尺寸	A3
圖號	I1A6-01
比例	1 : 50
日期	02/07/25

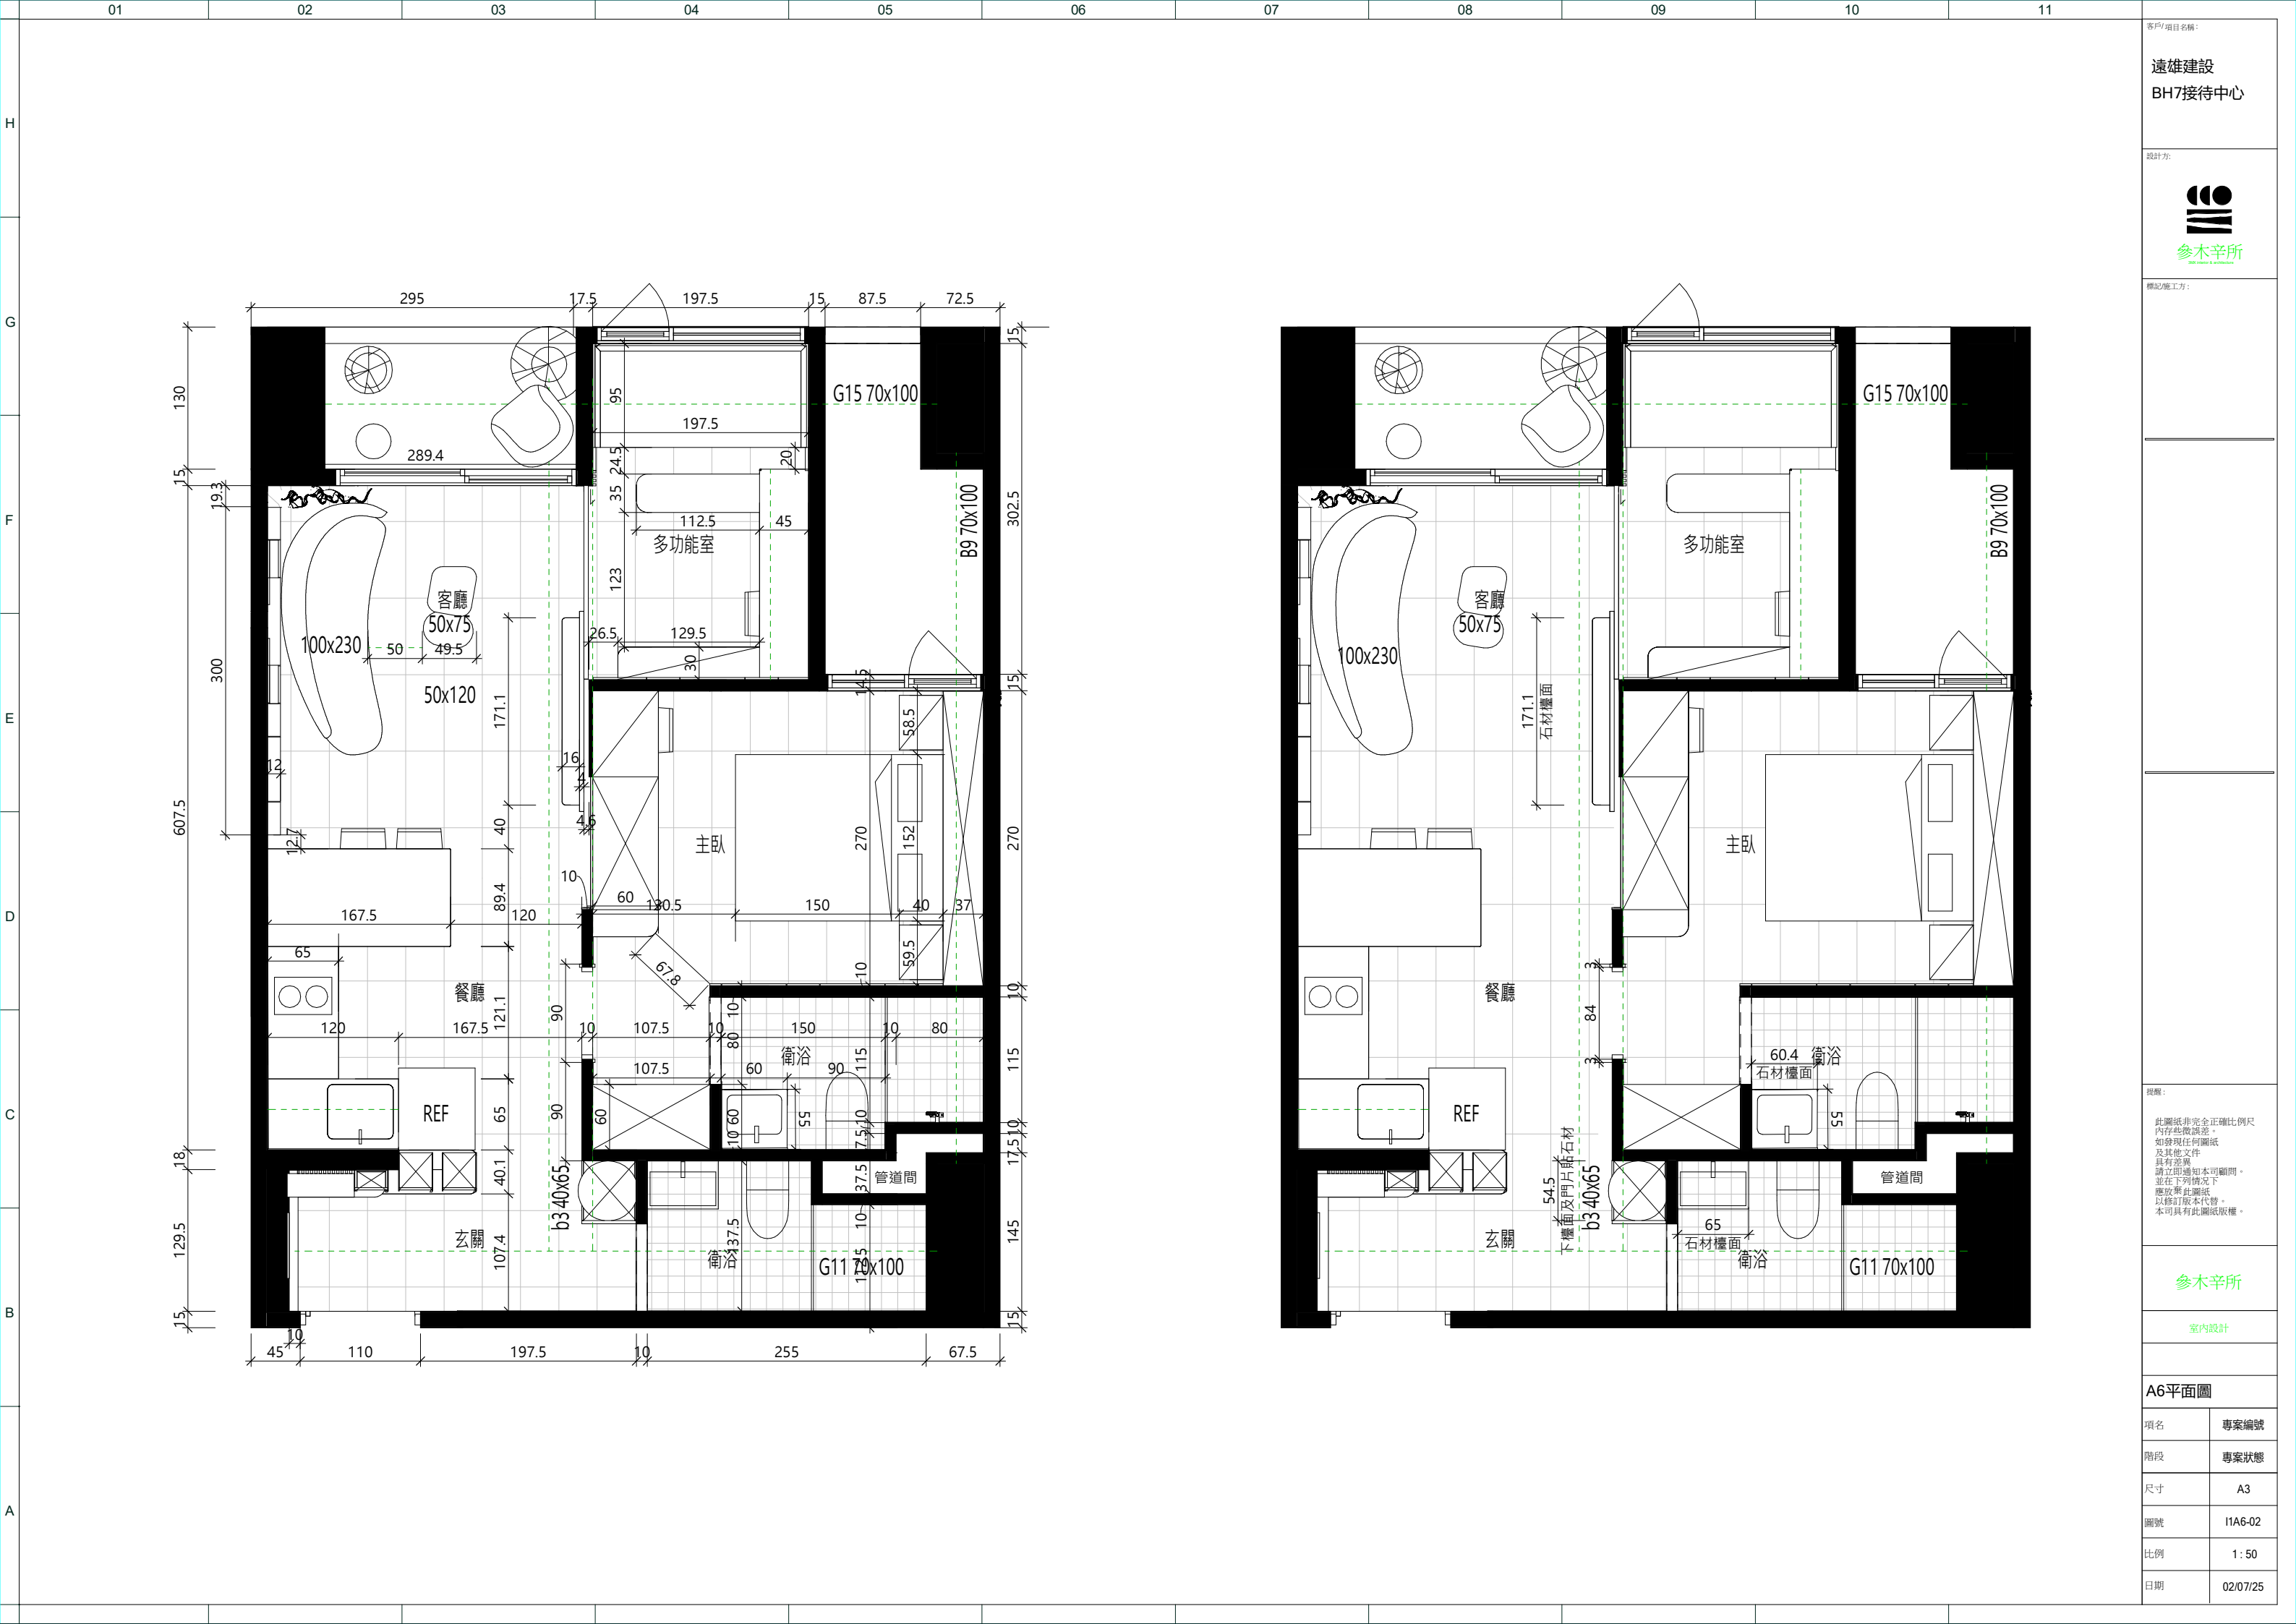

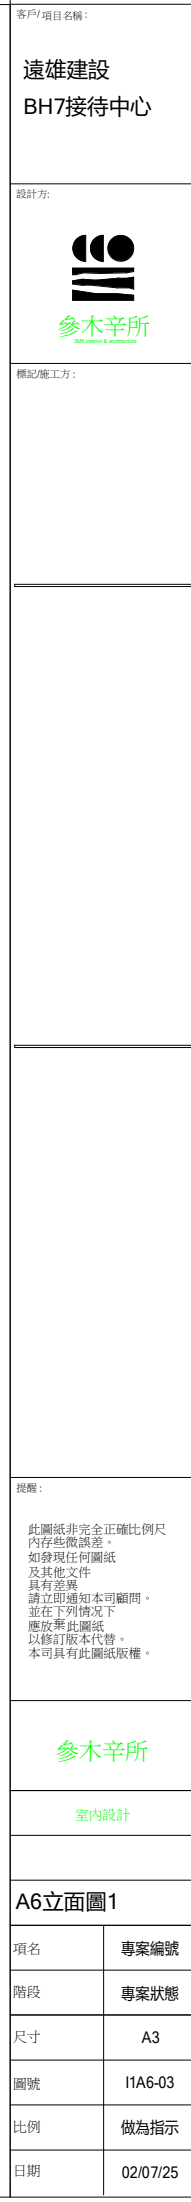

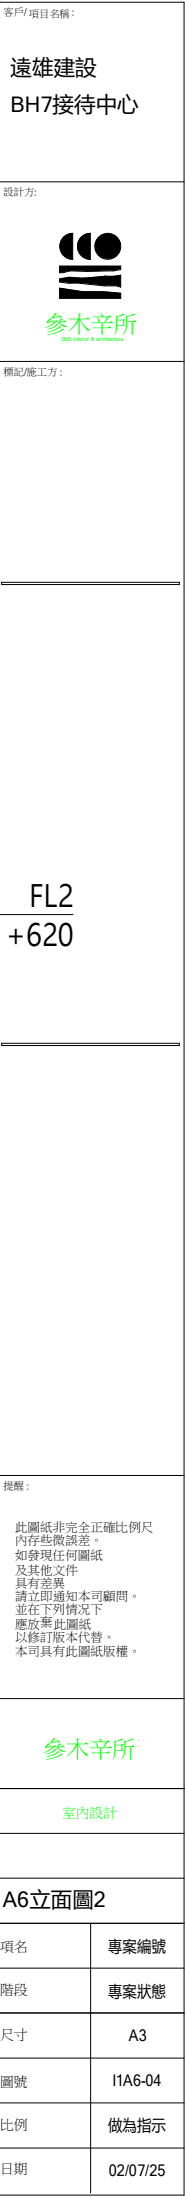

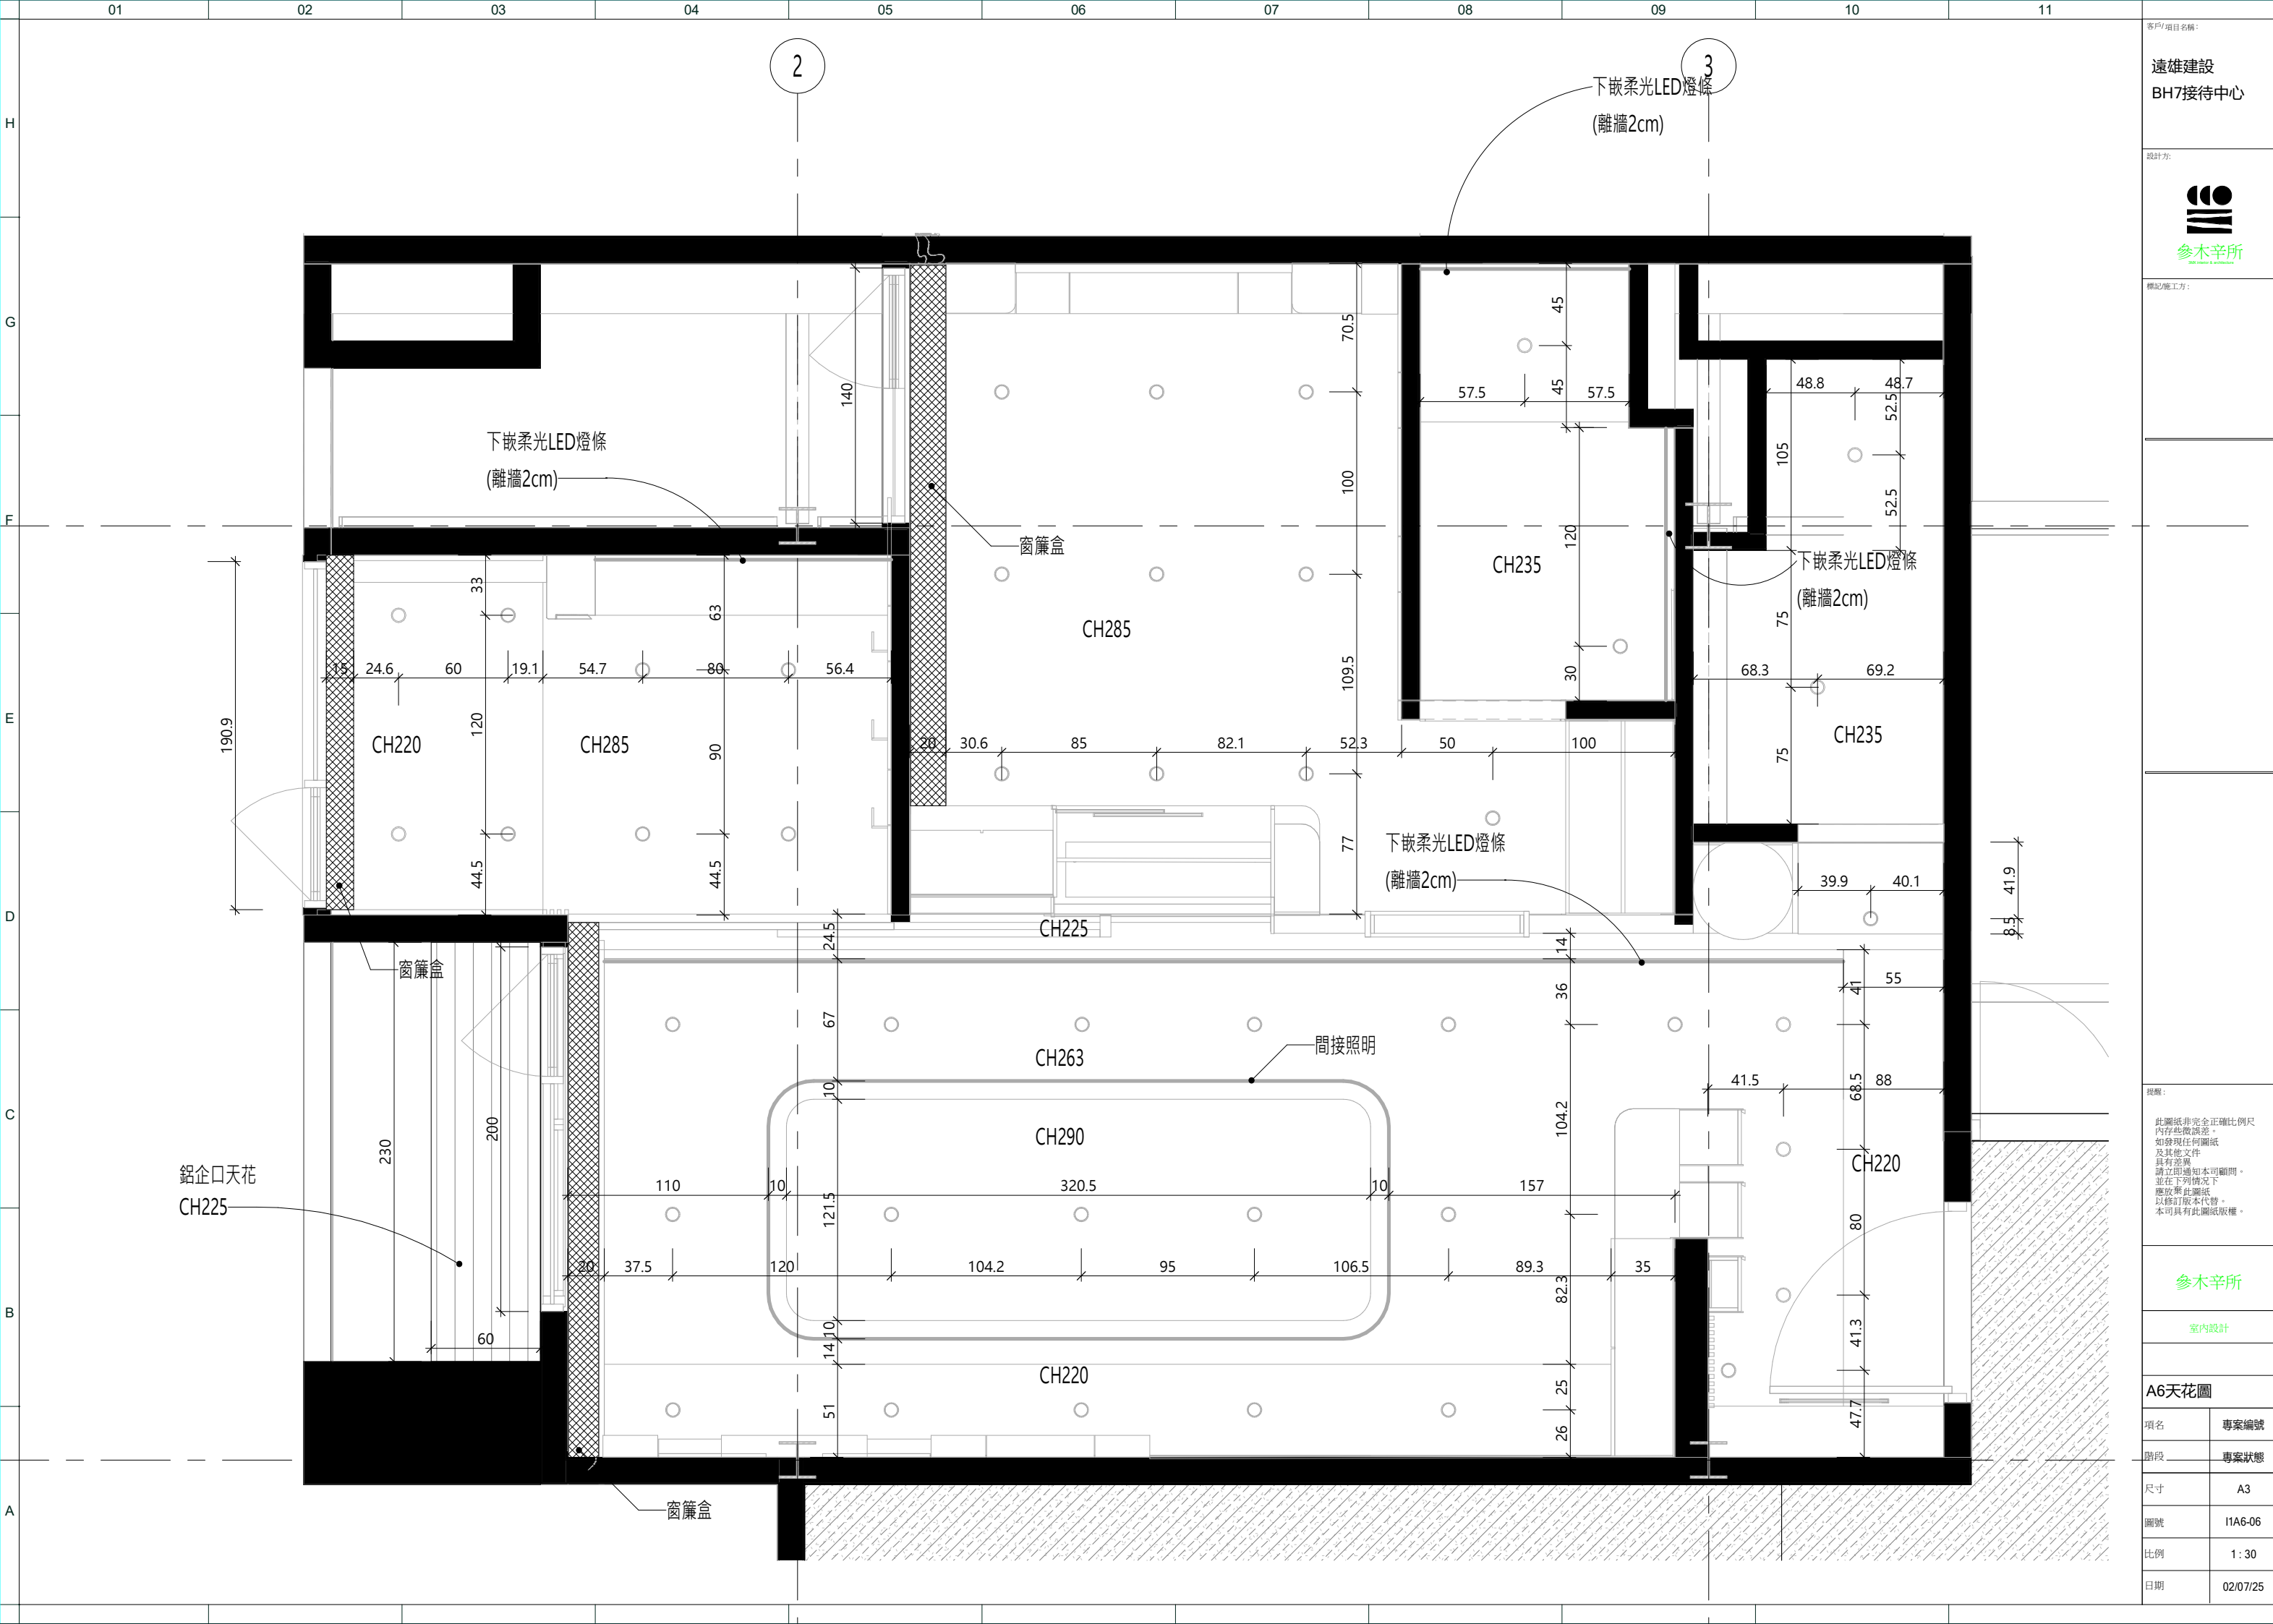

客戶/項目名稱:
遠雄建設
BH7接待中心

設計方:

參木辛所

標記/施工方:

提報:
此圖紙非完全正確比例尺
內存些微誤差。
如發現任何圖紙
及其他文件
具有差異
請立即通知本司顧問。
並在下列情況下
應放棄此圖紙
以修訂版本代替。
本司具有此圖紙版權。

參木辛所

室內設計

A6天花圖

項名	專案編號
階段	專案狀態
尺寸	A3
圖號	11A6-06
比例	1 : 30
日期	02/07/25

遠雄建設
BH7接待中心

設計方:



標記/施工方:

提醒:


此圖紙非完全正確比例尺
內存些微誤差。
如發現任何圖紙
及其他文件
具有差異
請立即通知本司顧問。
並在下列情況下
應放棄此圖紙
以修訂版本代替。
本司具有此圖紙版權。

參木辛所

室內設計


A6櫃體圖1

項名	專案編號
階段	專案狀態
尺寸	A3
圖號	11A6-07
比例	1 : 30
日期	02/07/25

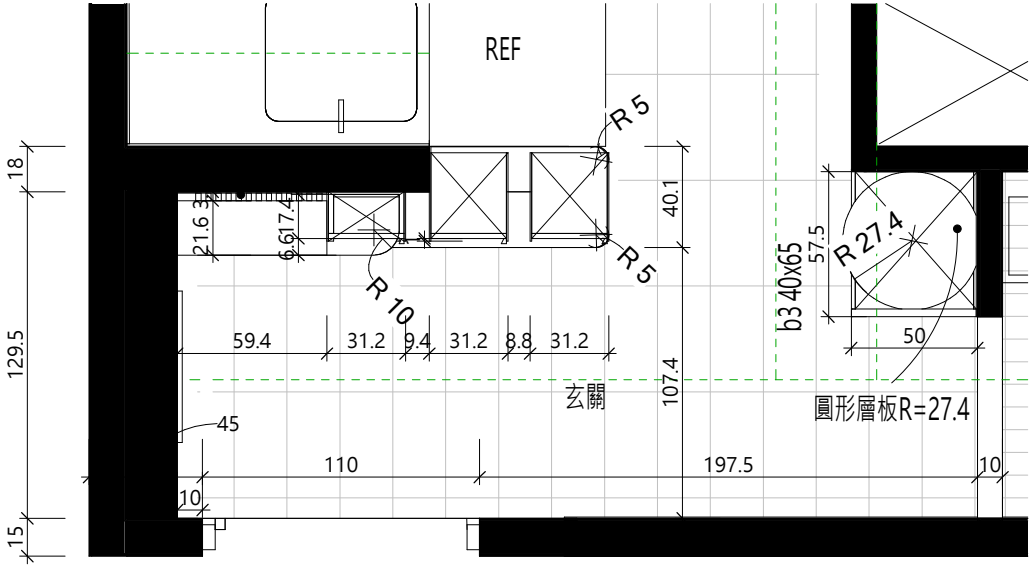


櫃體圖1

A1=NTS A3=NTS

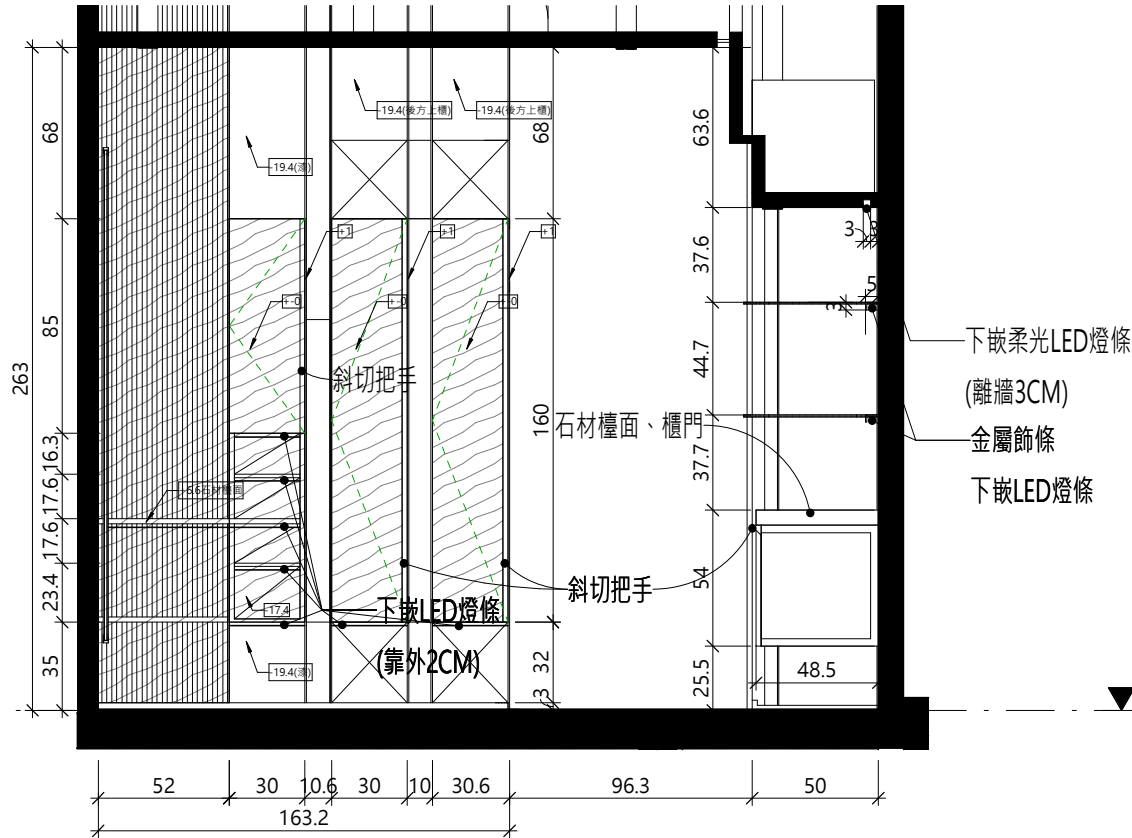

櫃體圖1

A1=NTS A3=NTS


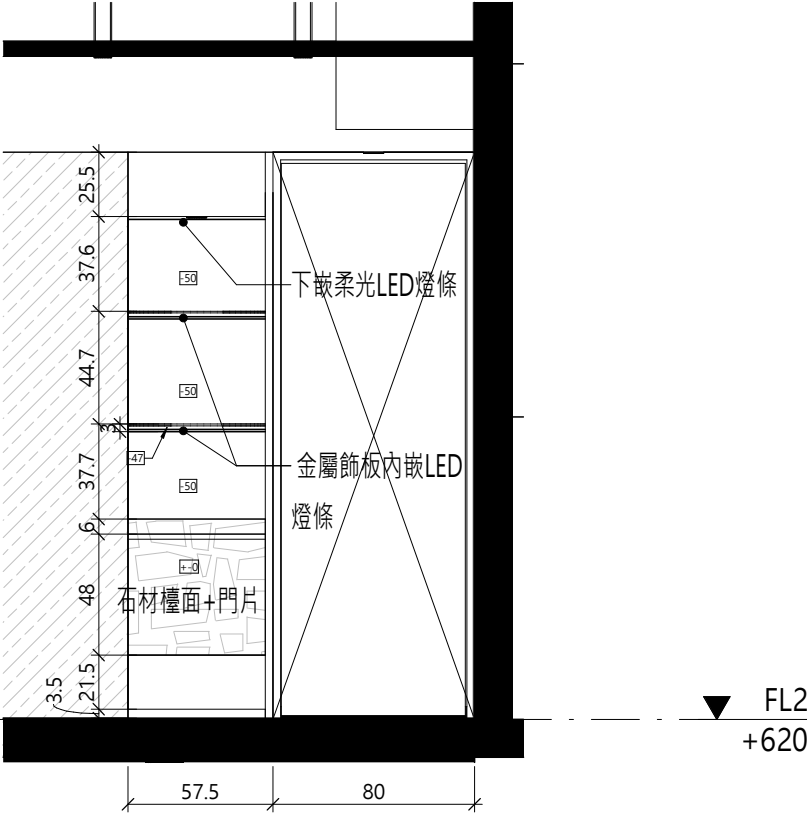


櫃體圖1


A1=NTS A3=NTS

FL2
+620

FL2
+620

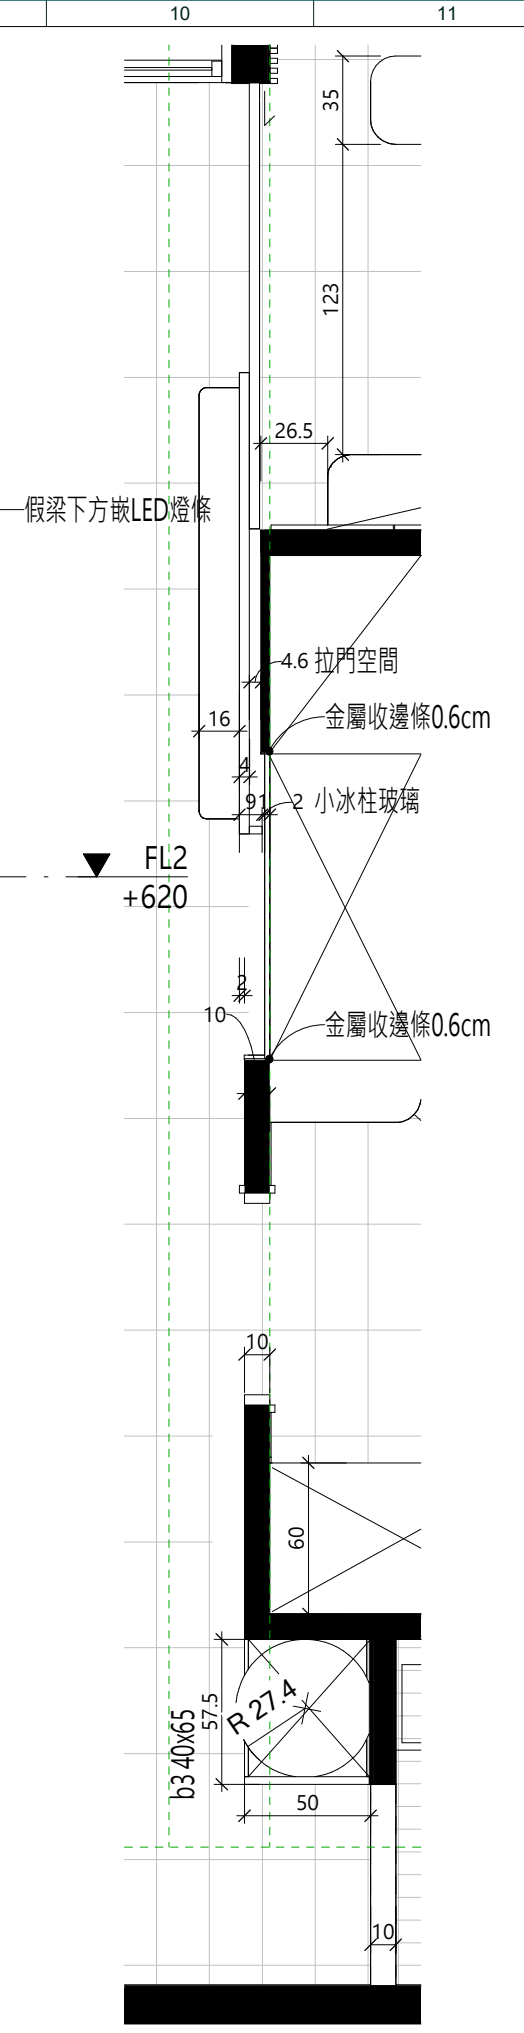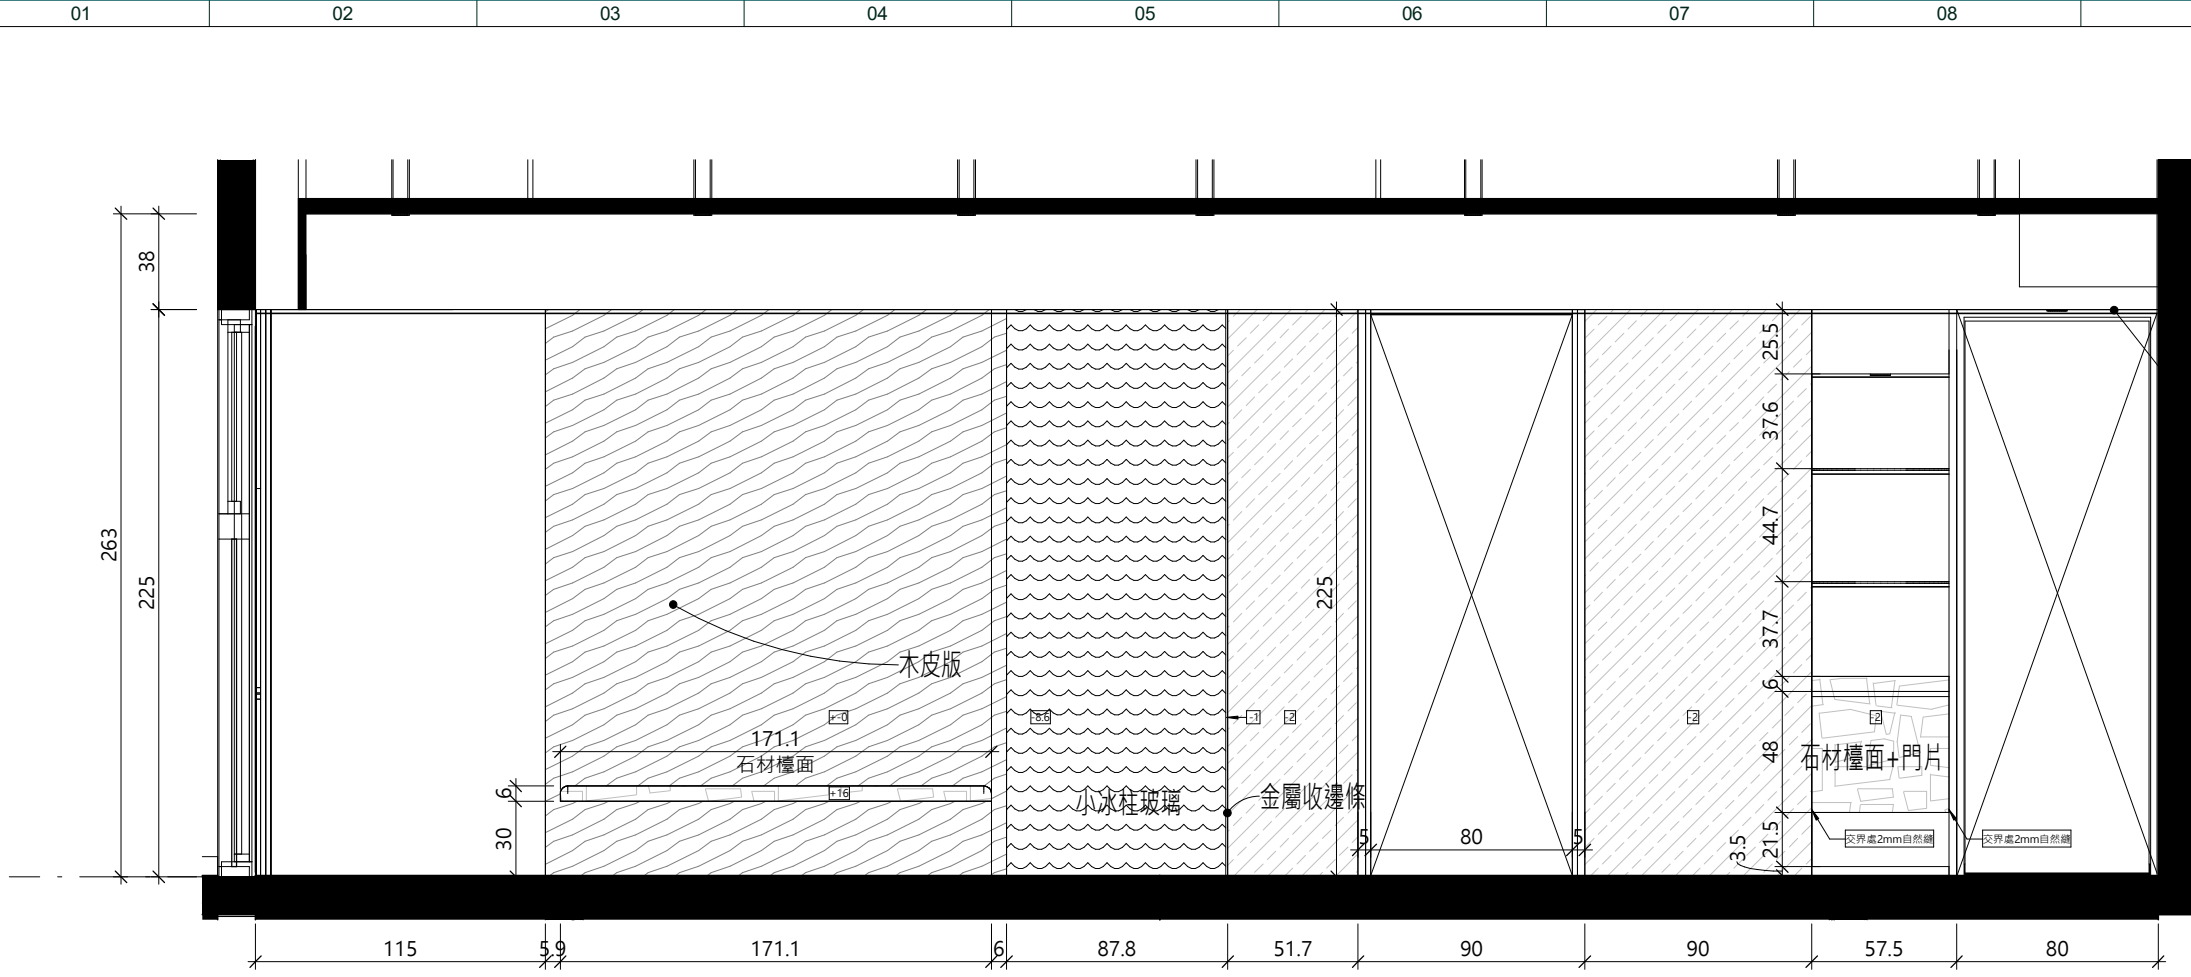


2 櫃體圖2
A1=NTS A3=NTS

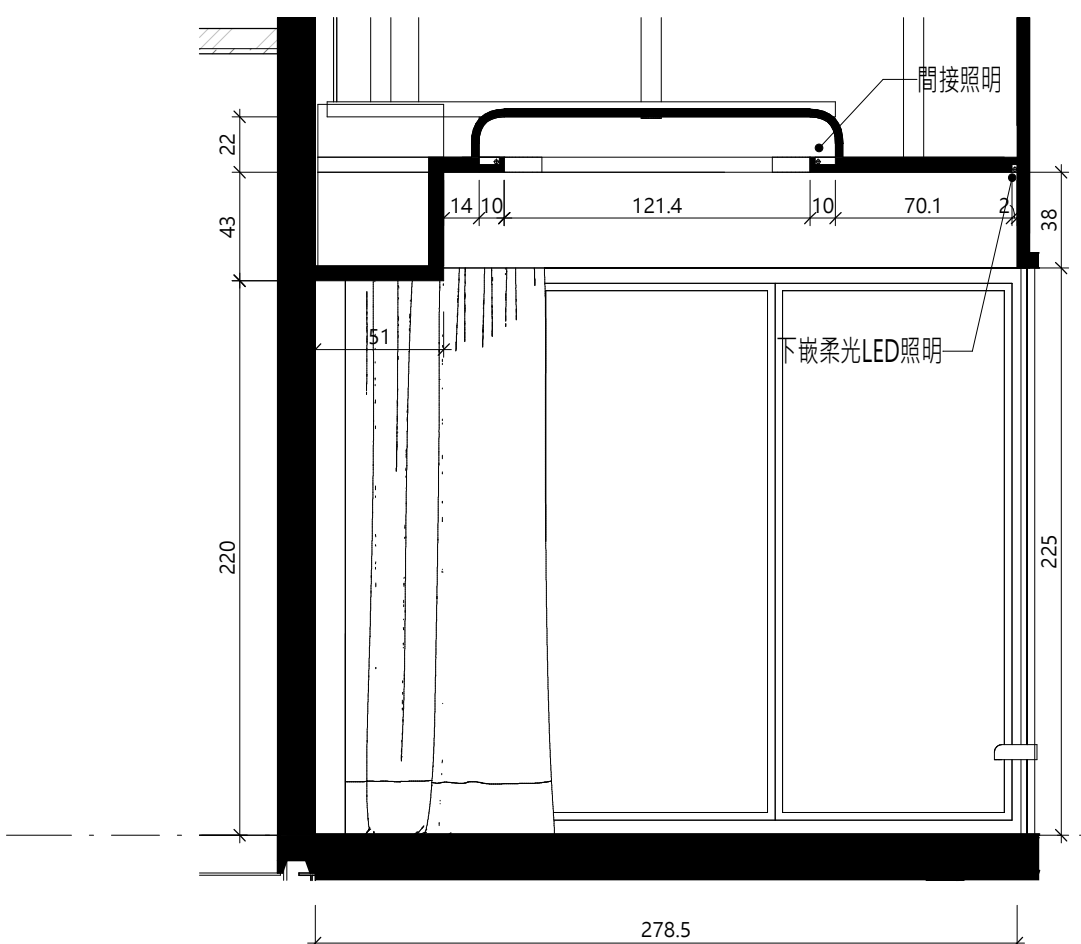

3 天花詳圖
A1=NTS A3=NTS

1 櫃體圖2
A1=NTS A3=NTS


客戶/項目名稱: 遠雄建設 BH7接待中心	
設計方: 	
標記/施工方:	
說明: 此圖紙非完全正確比例尺 內存些微誤差。 如發現任何圖紙 及其他文件 具有差異 請立即通知本司顧問。 並在下列情況下 應放棄此圖紙 以修訂版本代替。 本司具有此圖紙版權。	
參木辛所	
室內設計	
A6櫃體圖2	
項名	專案編號
階段	專案狀態
尺寸	A3
圖號	11A6-08
比例	1:30
日期	02/07/25

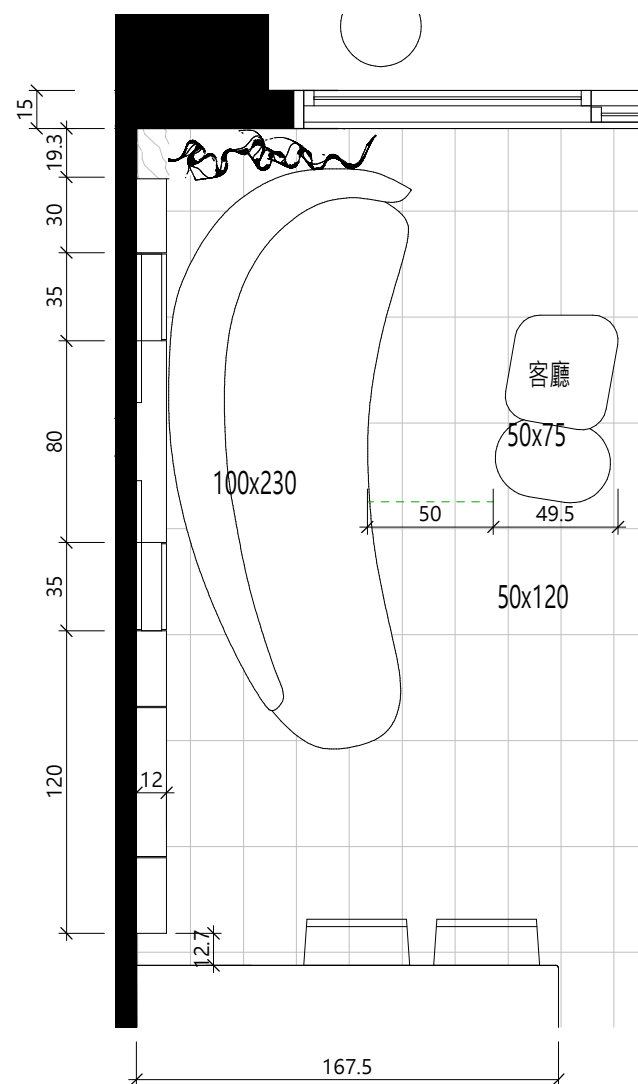

沙發背櫃

A1=NTS


A3=NTS

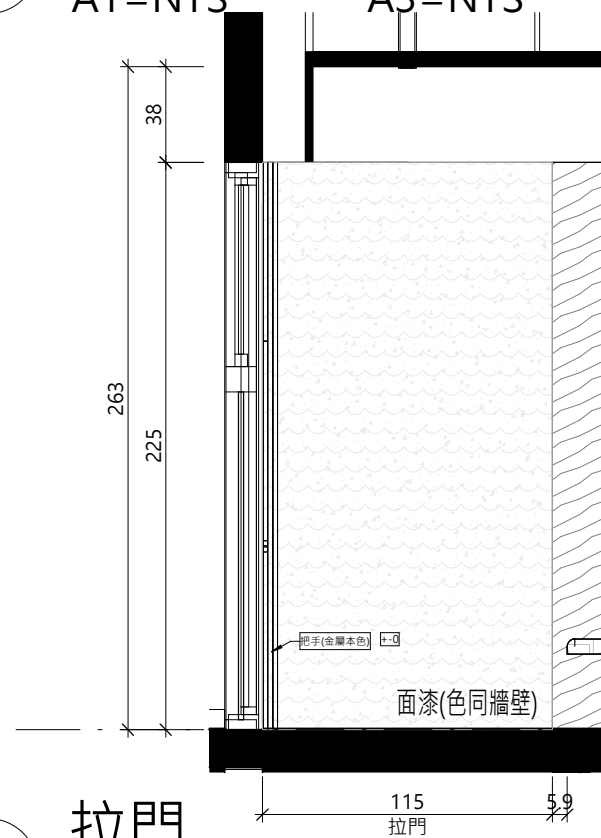

拉門

A1=NTS


A3=NTS

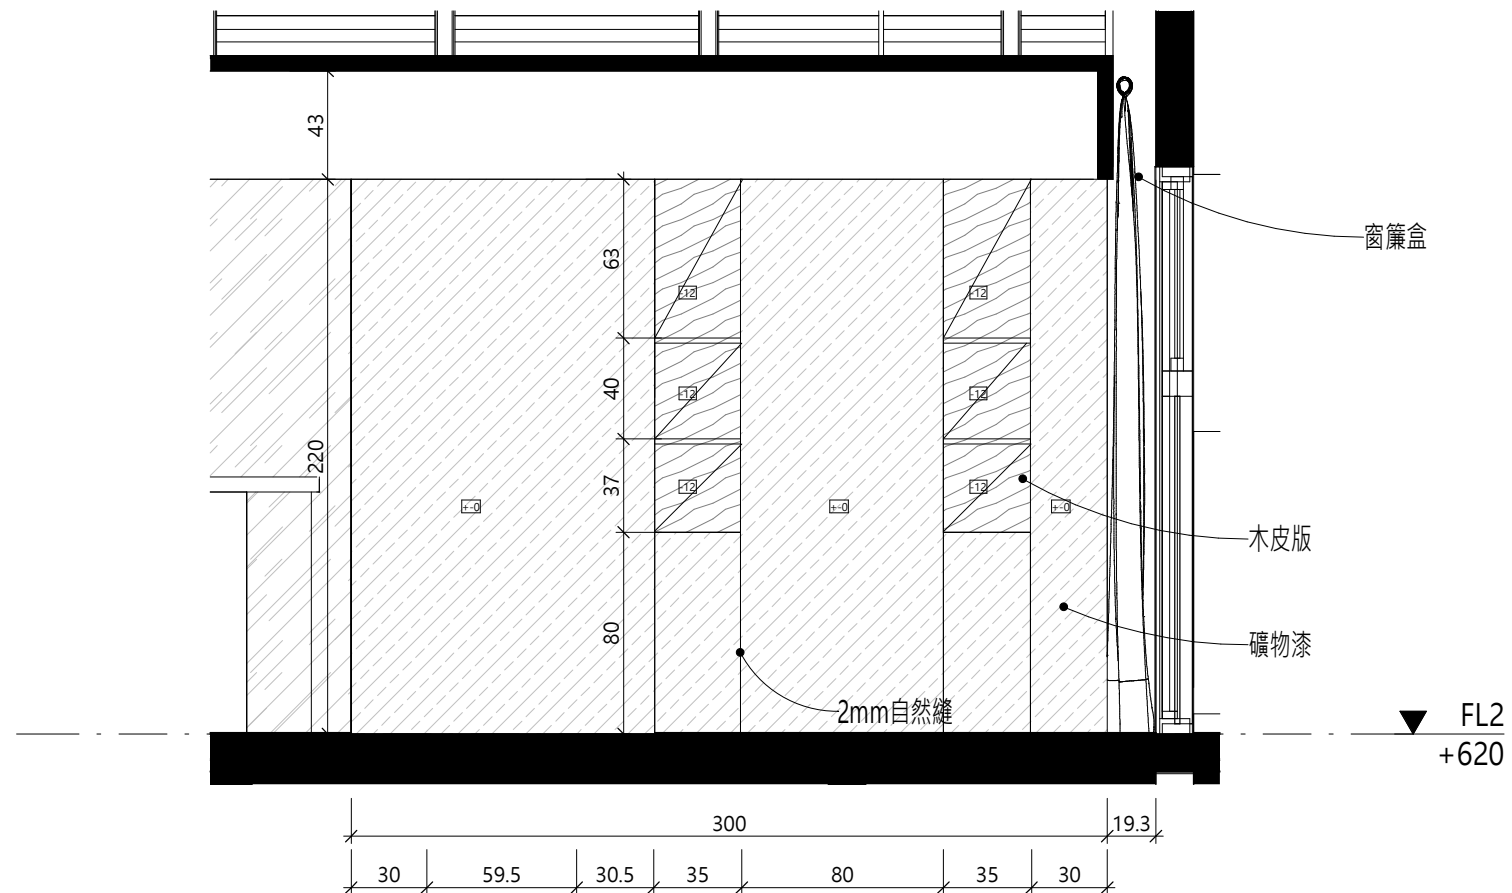

沙發背櫃

A1=NTS


A3=NTS

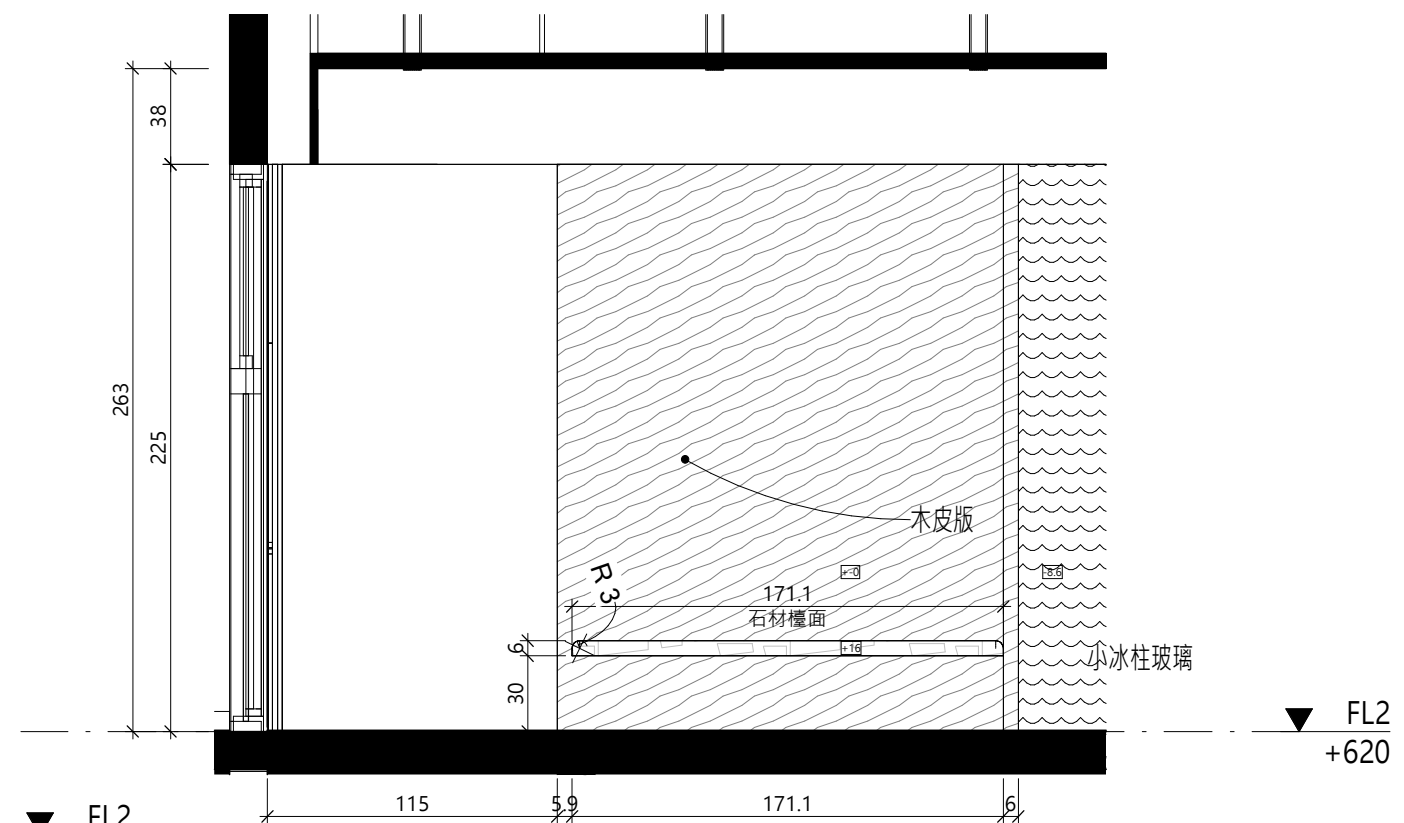

電視櫃

A1=NTS






A3=NTS

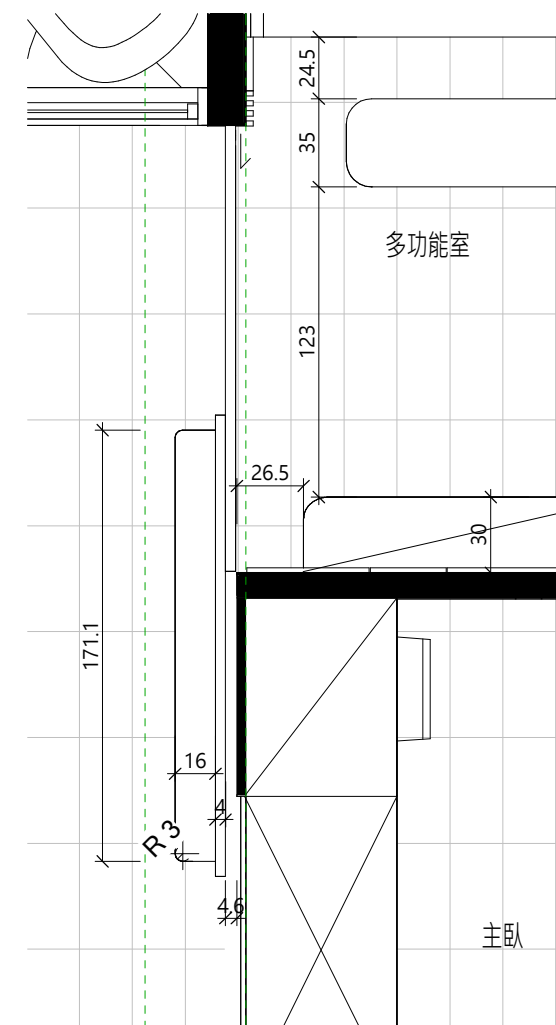

電視櫃

A1=NTS

A3=NTS

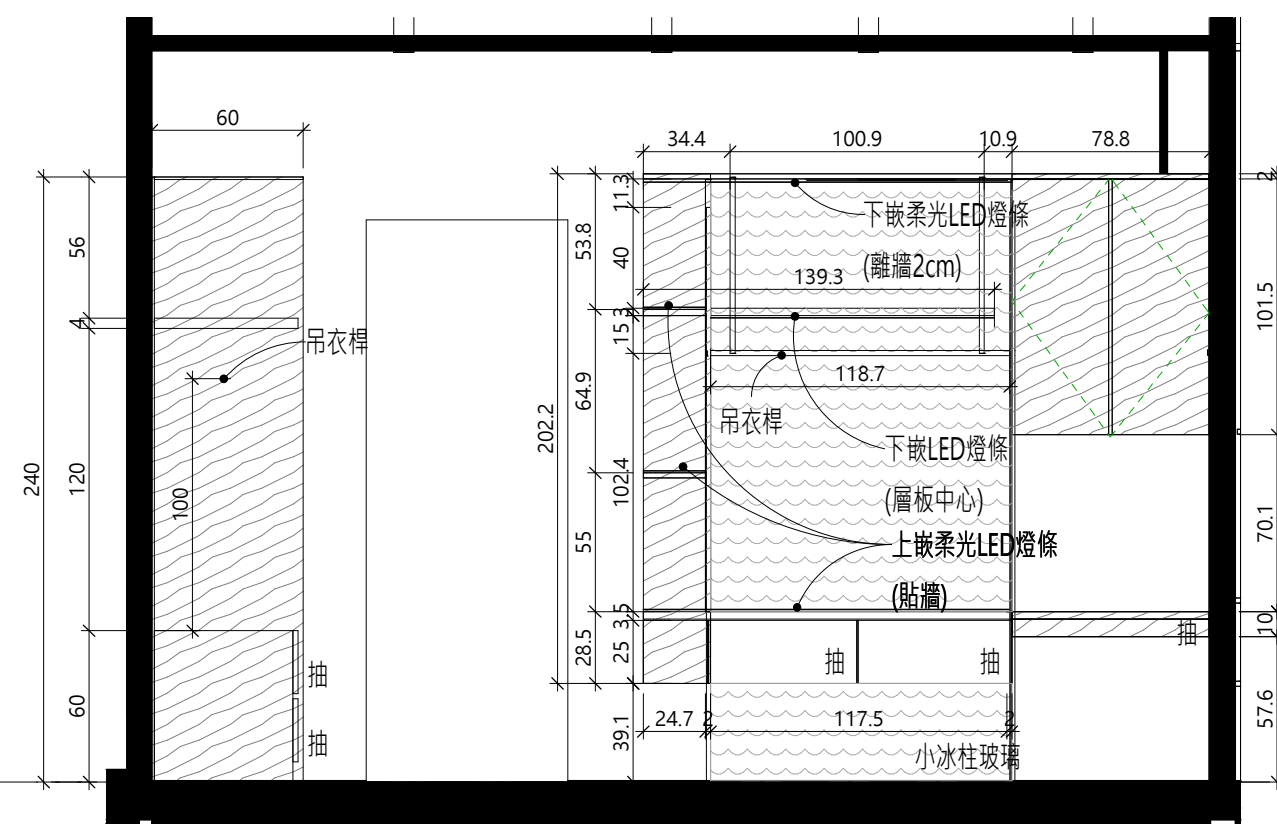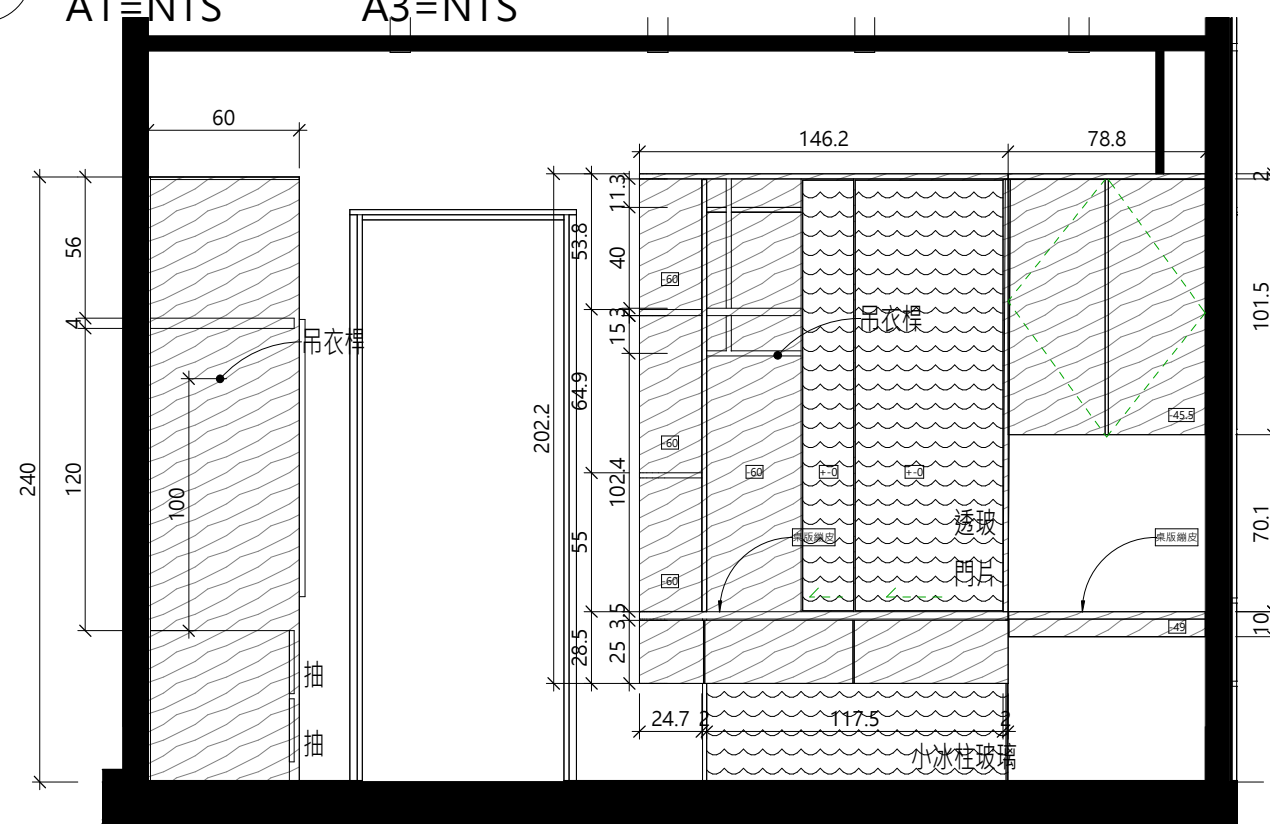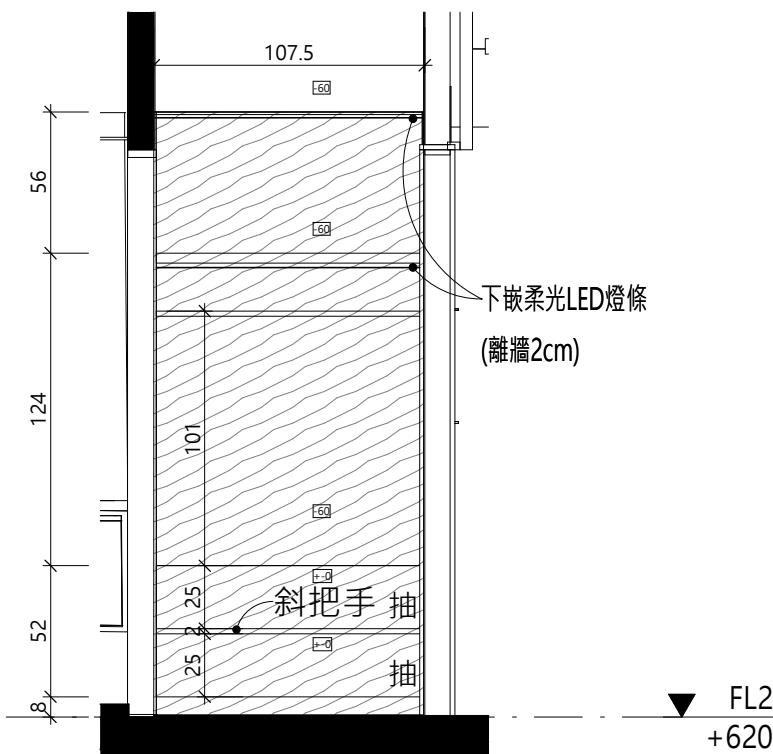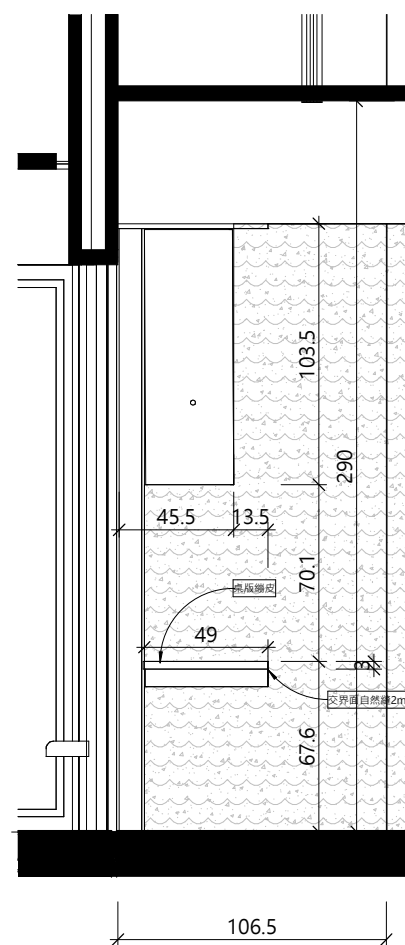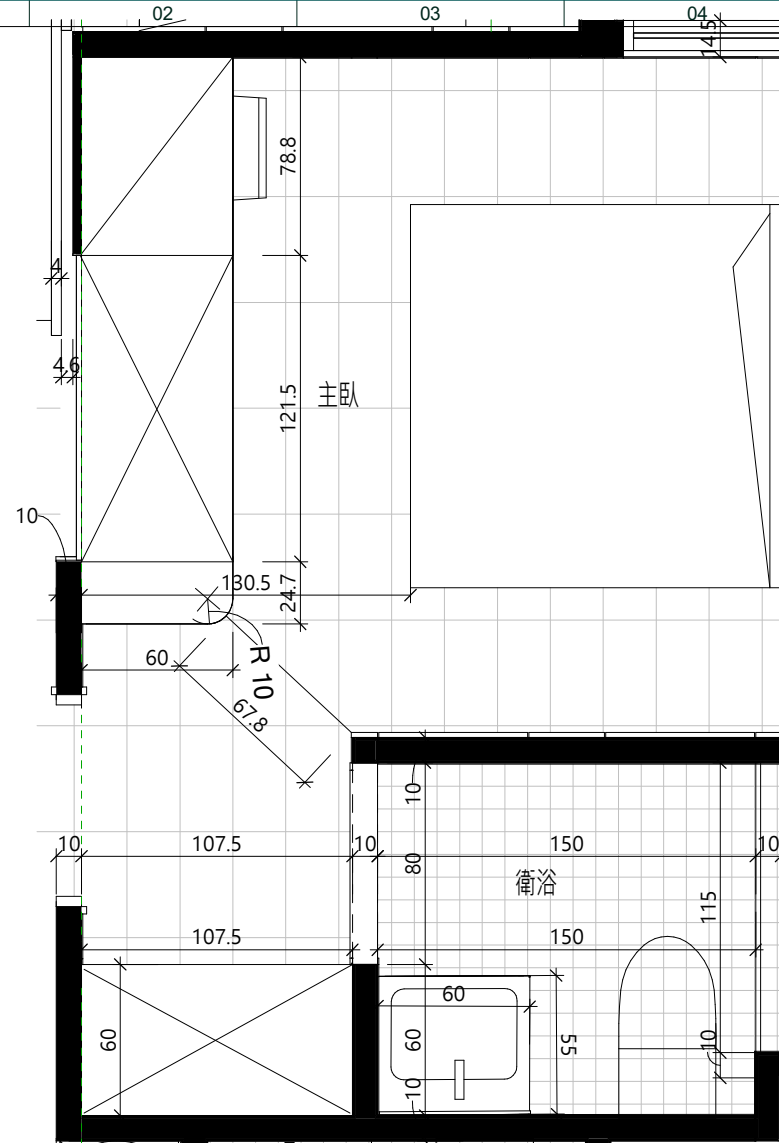

客戶/項目名稱:	
----------	--

設計方:

標記/施工方:

提醒：

此圖紙非完全正確比例
內存些微誤差。
如發現任何圖紙
及其他文件
具有差異
請立即通知本司顧問。
並在下列情況下
應放棄此圖紙
以修訂版本代替。
本司具有此圖紙版權。

魚木立所

室內設計

A6櫃體圖4


項名	專案編號
----	------

▼	El 2	事实非然
---	------	------

圖號	I1A6-10
----	---------

比例	1:30
----	------

日期	02/07/25
----	----------

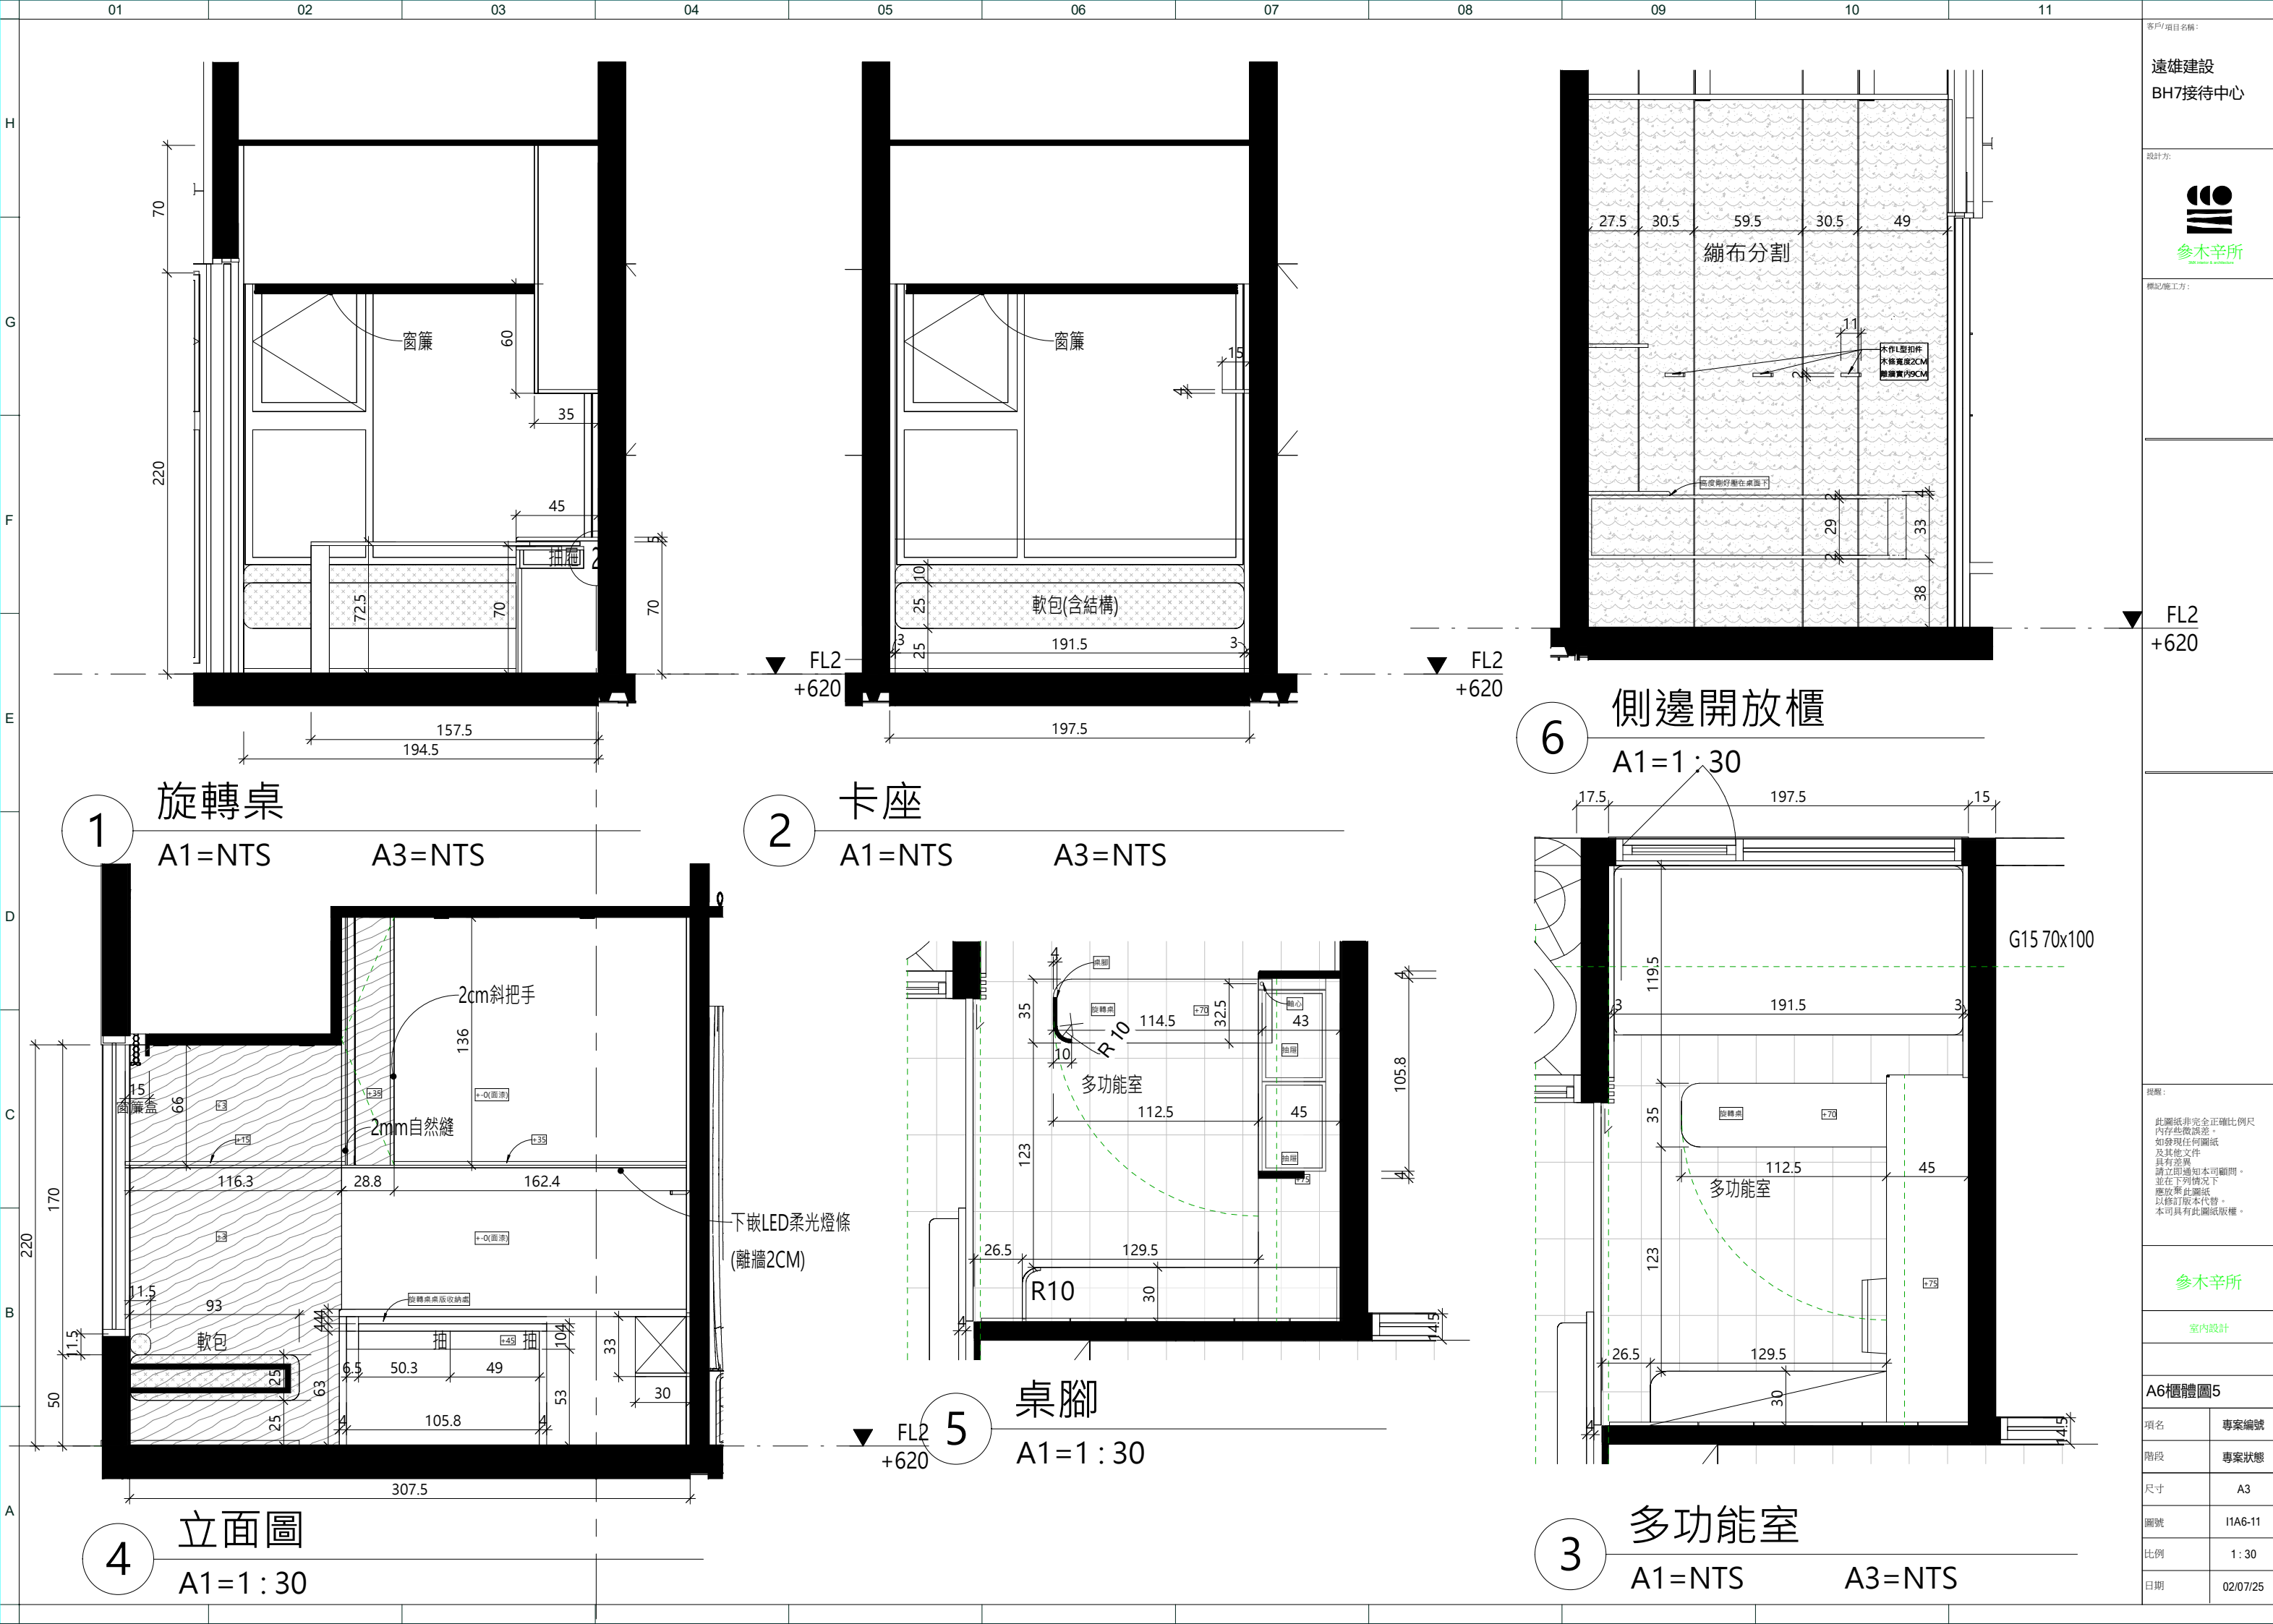

客戶/項目名稱:	
遠雄建設 BH7接待中心	
設計方:	
標記/施工方:	
FL2 +620	
6 側邊開放櫃 A1=1:30	
17.5 197.5 15 119.5 191.5 3 35 112.5 45 26.5 129.5 30 14.5	
G15 70x100	
此圖紙非完全正確比例尺 內存些微誤差。 如發現任何圖紙 及其他文件 具有差異 請立即通知本司顧問。 並在下列情況下 應放棄此圖紙 以修訂版本代替。 本司具有此圖紙版權。	
參木辛所	
室內設計	
A6櫃體圖5	
項名	專案編號
階段	專案狀態
尺寸	A3
圖號	11A6-11
比例	1:30
日期	02/07/25



客戶/項目名稱:
遠雄建設
BH7接待中心

設計方:

標記/施工方:

此圖紙非完全正確比例尺
內存些微誤差
如發現任何圖紙
及其他文件
具有差異
請立即通知本司顧問。
並在下列情況下
應放棄此圖紙
以修訂版本代替。
本司具有此圖紙版權。

參木辛所

室內設計

A11建照圖、隔間尺寸圖

項名	專案編號
階段	專案狀態
尺寸	A3
圖號	11A11-00
比例	1 : 50
日期	02/07/25



客戶/項目名稱:
遠雄建設
BH7接待中心

設計方:

標記/施工方:


規製:
此圖紙非完全正確比例尺
內存些微誤差。
如發現任何圖紙
及其他文件
具有差異
請立即通知本司顧問。
並在下列情況下
應放棄此圖紙
以修訂版本代替。
本司具有此圖紙版權。


參木辛所

室內設計

A11平面圖

項名	專案編號
階段	專案狀態
尺寸	A3
圖號	I1A11-01
比例	1:50
日期	02/07/25

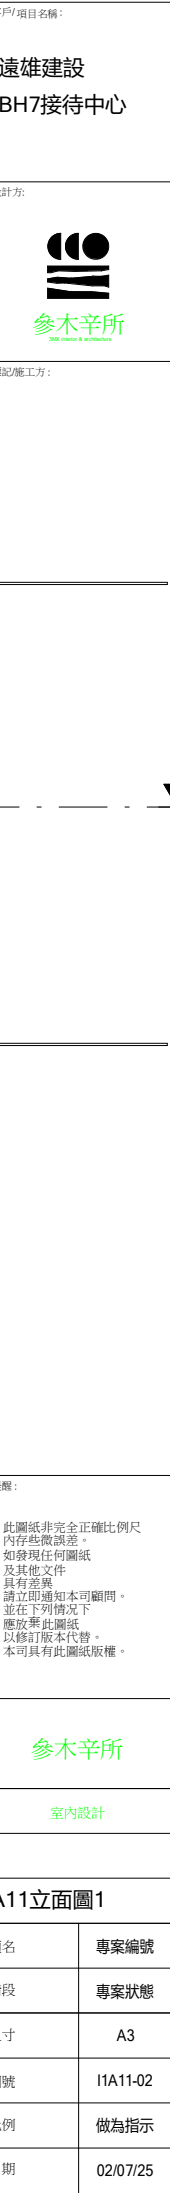

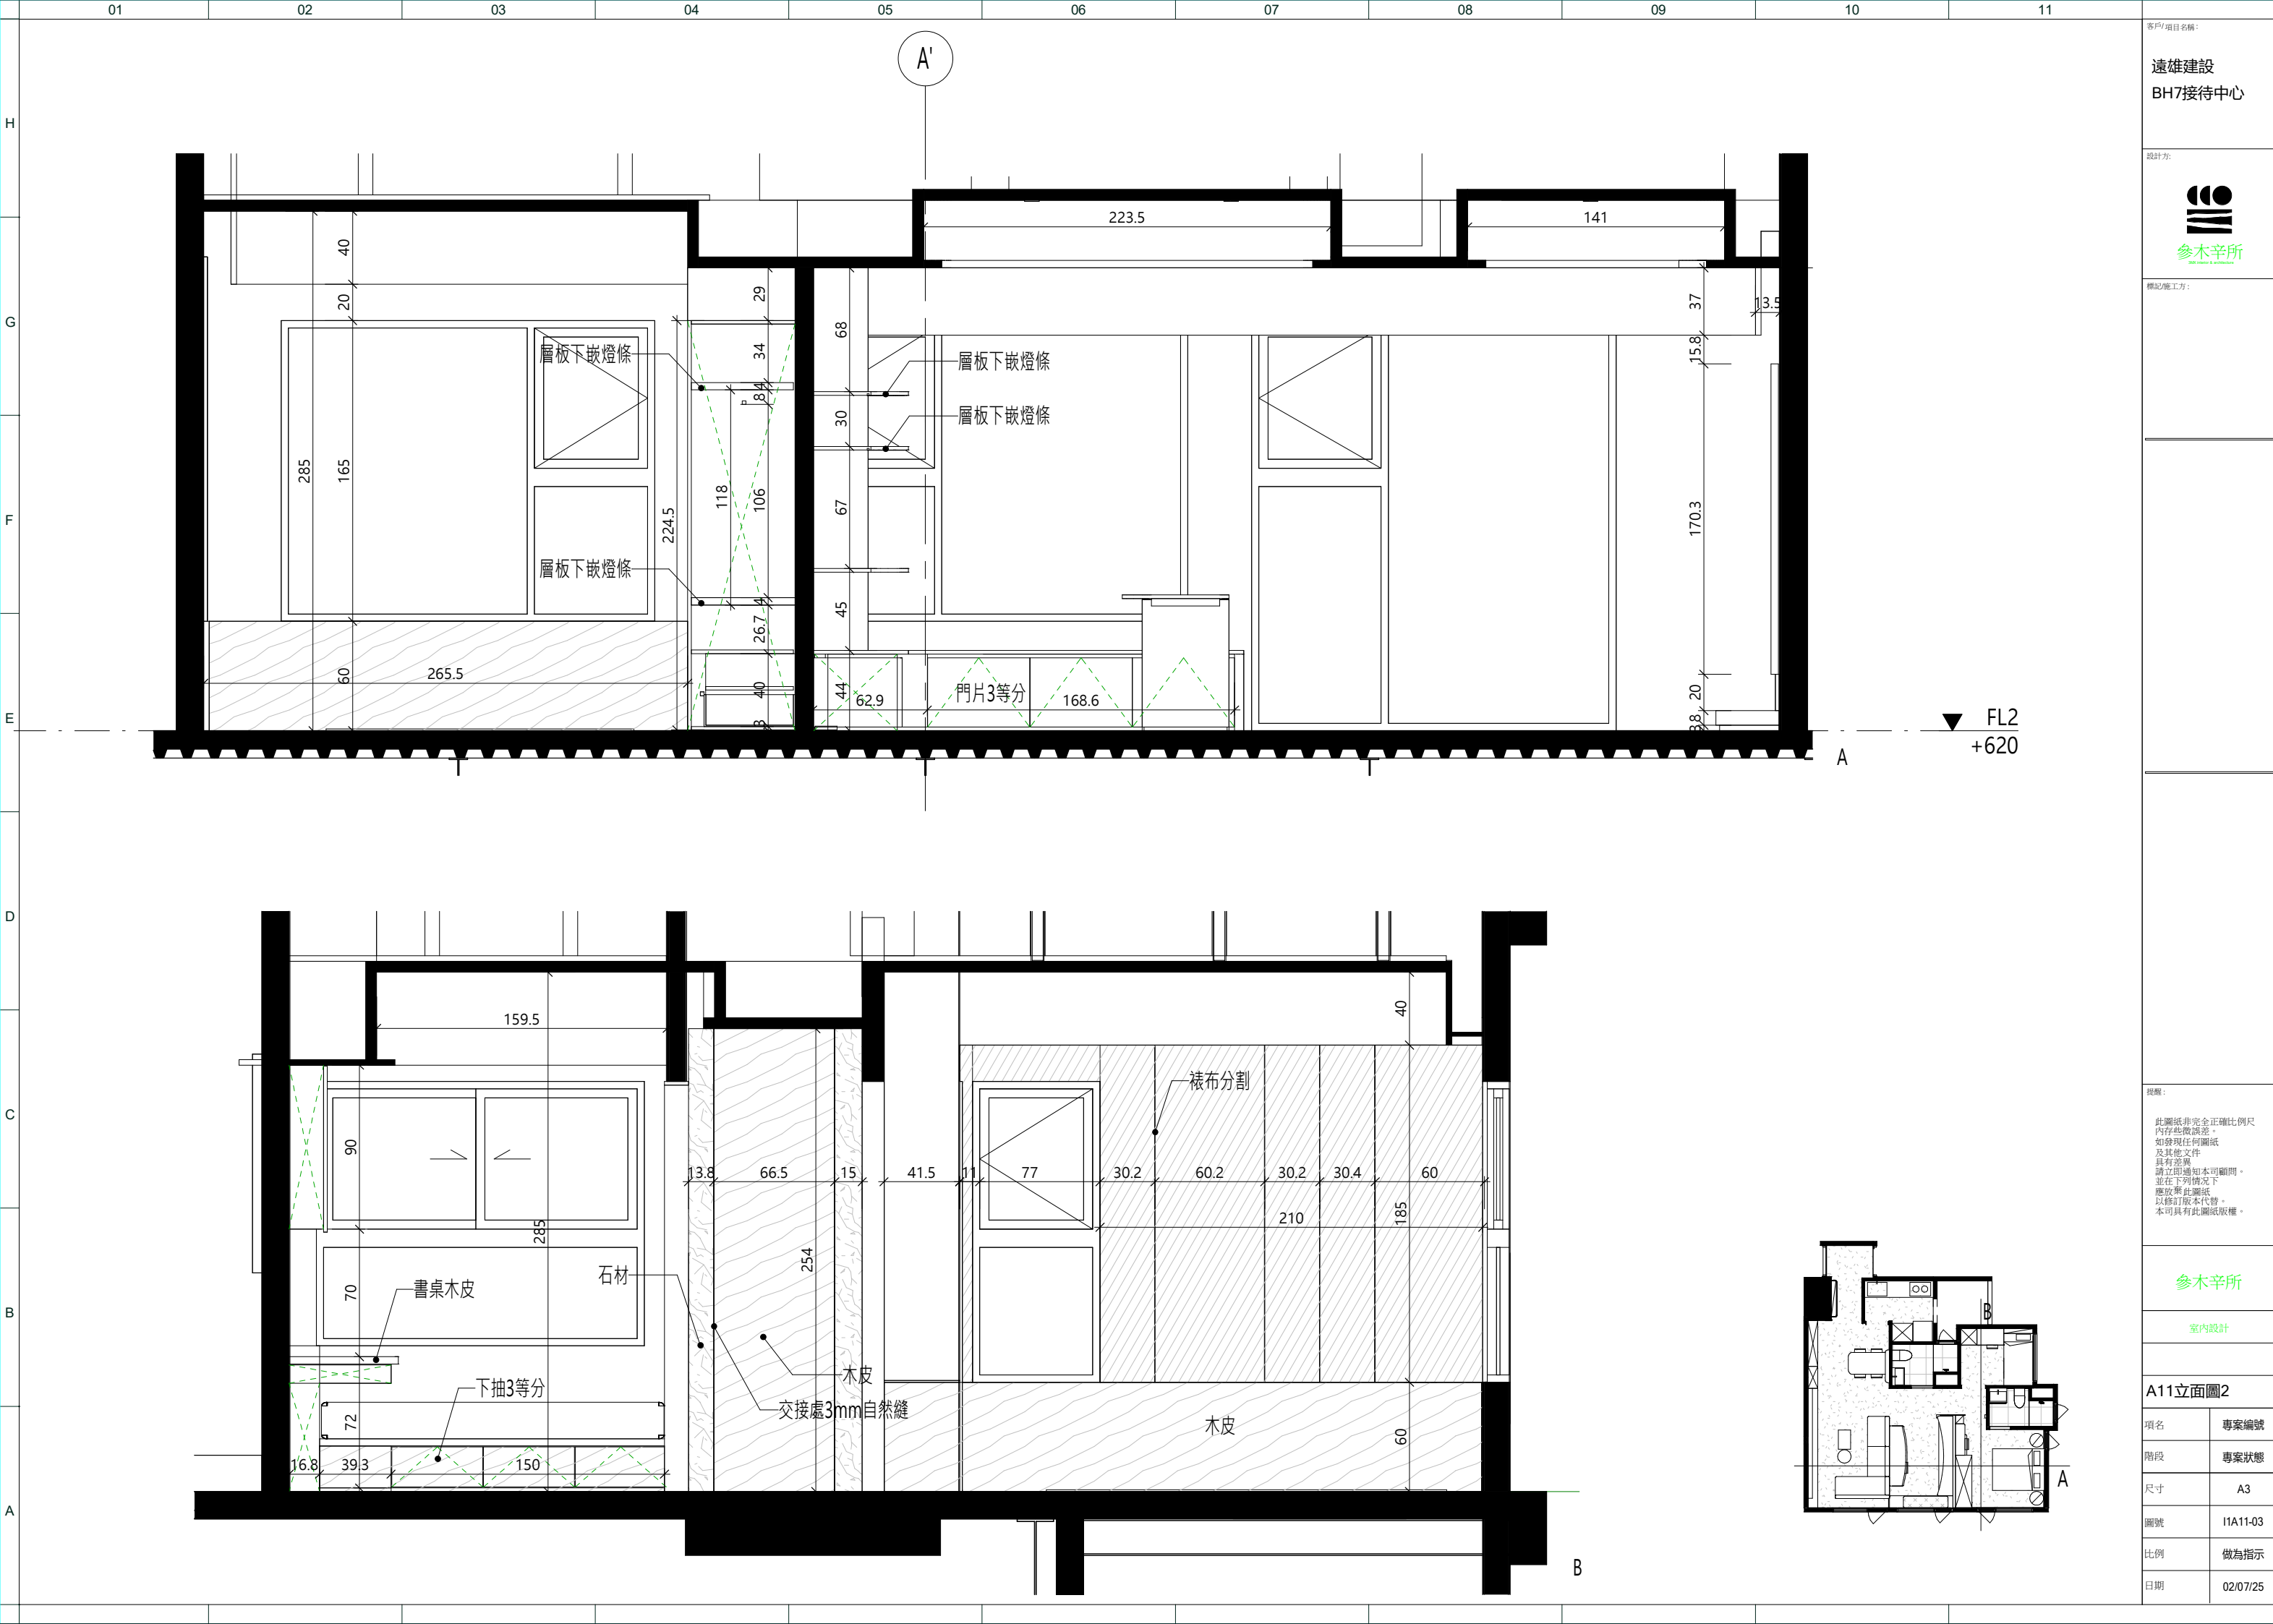

客戶/項目名稱：

遠雄建設
BH7接待中心

設計方：



標記/施工方：

提燈：


此圖紙非完全正確比例尺
內存些微誤差。
如發現任何圖紙
及其他文件
具有差異
請立即通知本司顧問。
並在下列情況下
應放棄此圖紙
以修訂版本代替。
本司具有此圖紙版權。

參木辛所

室內設計

A11立面圖2

項名	專案編號
階段	專案狀態
尺寸	A3
圖號	I1A11-03
比例	做為指示
日期	02/07/25

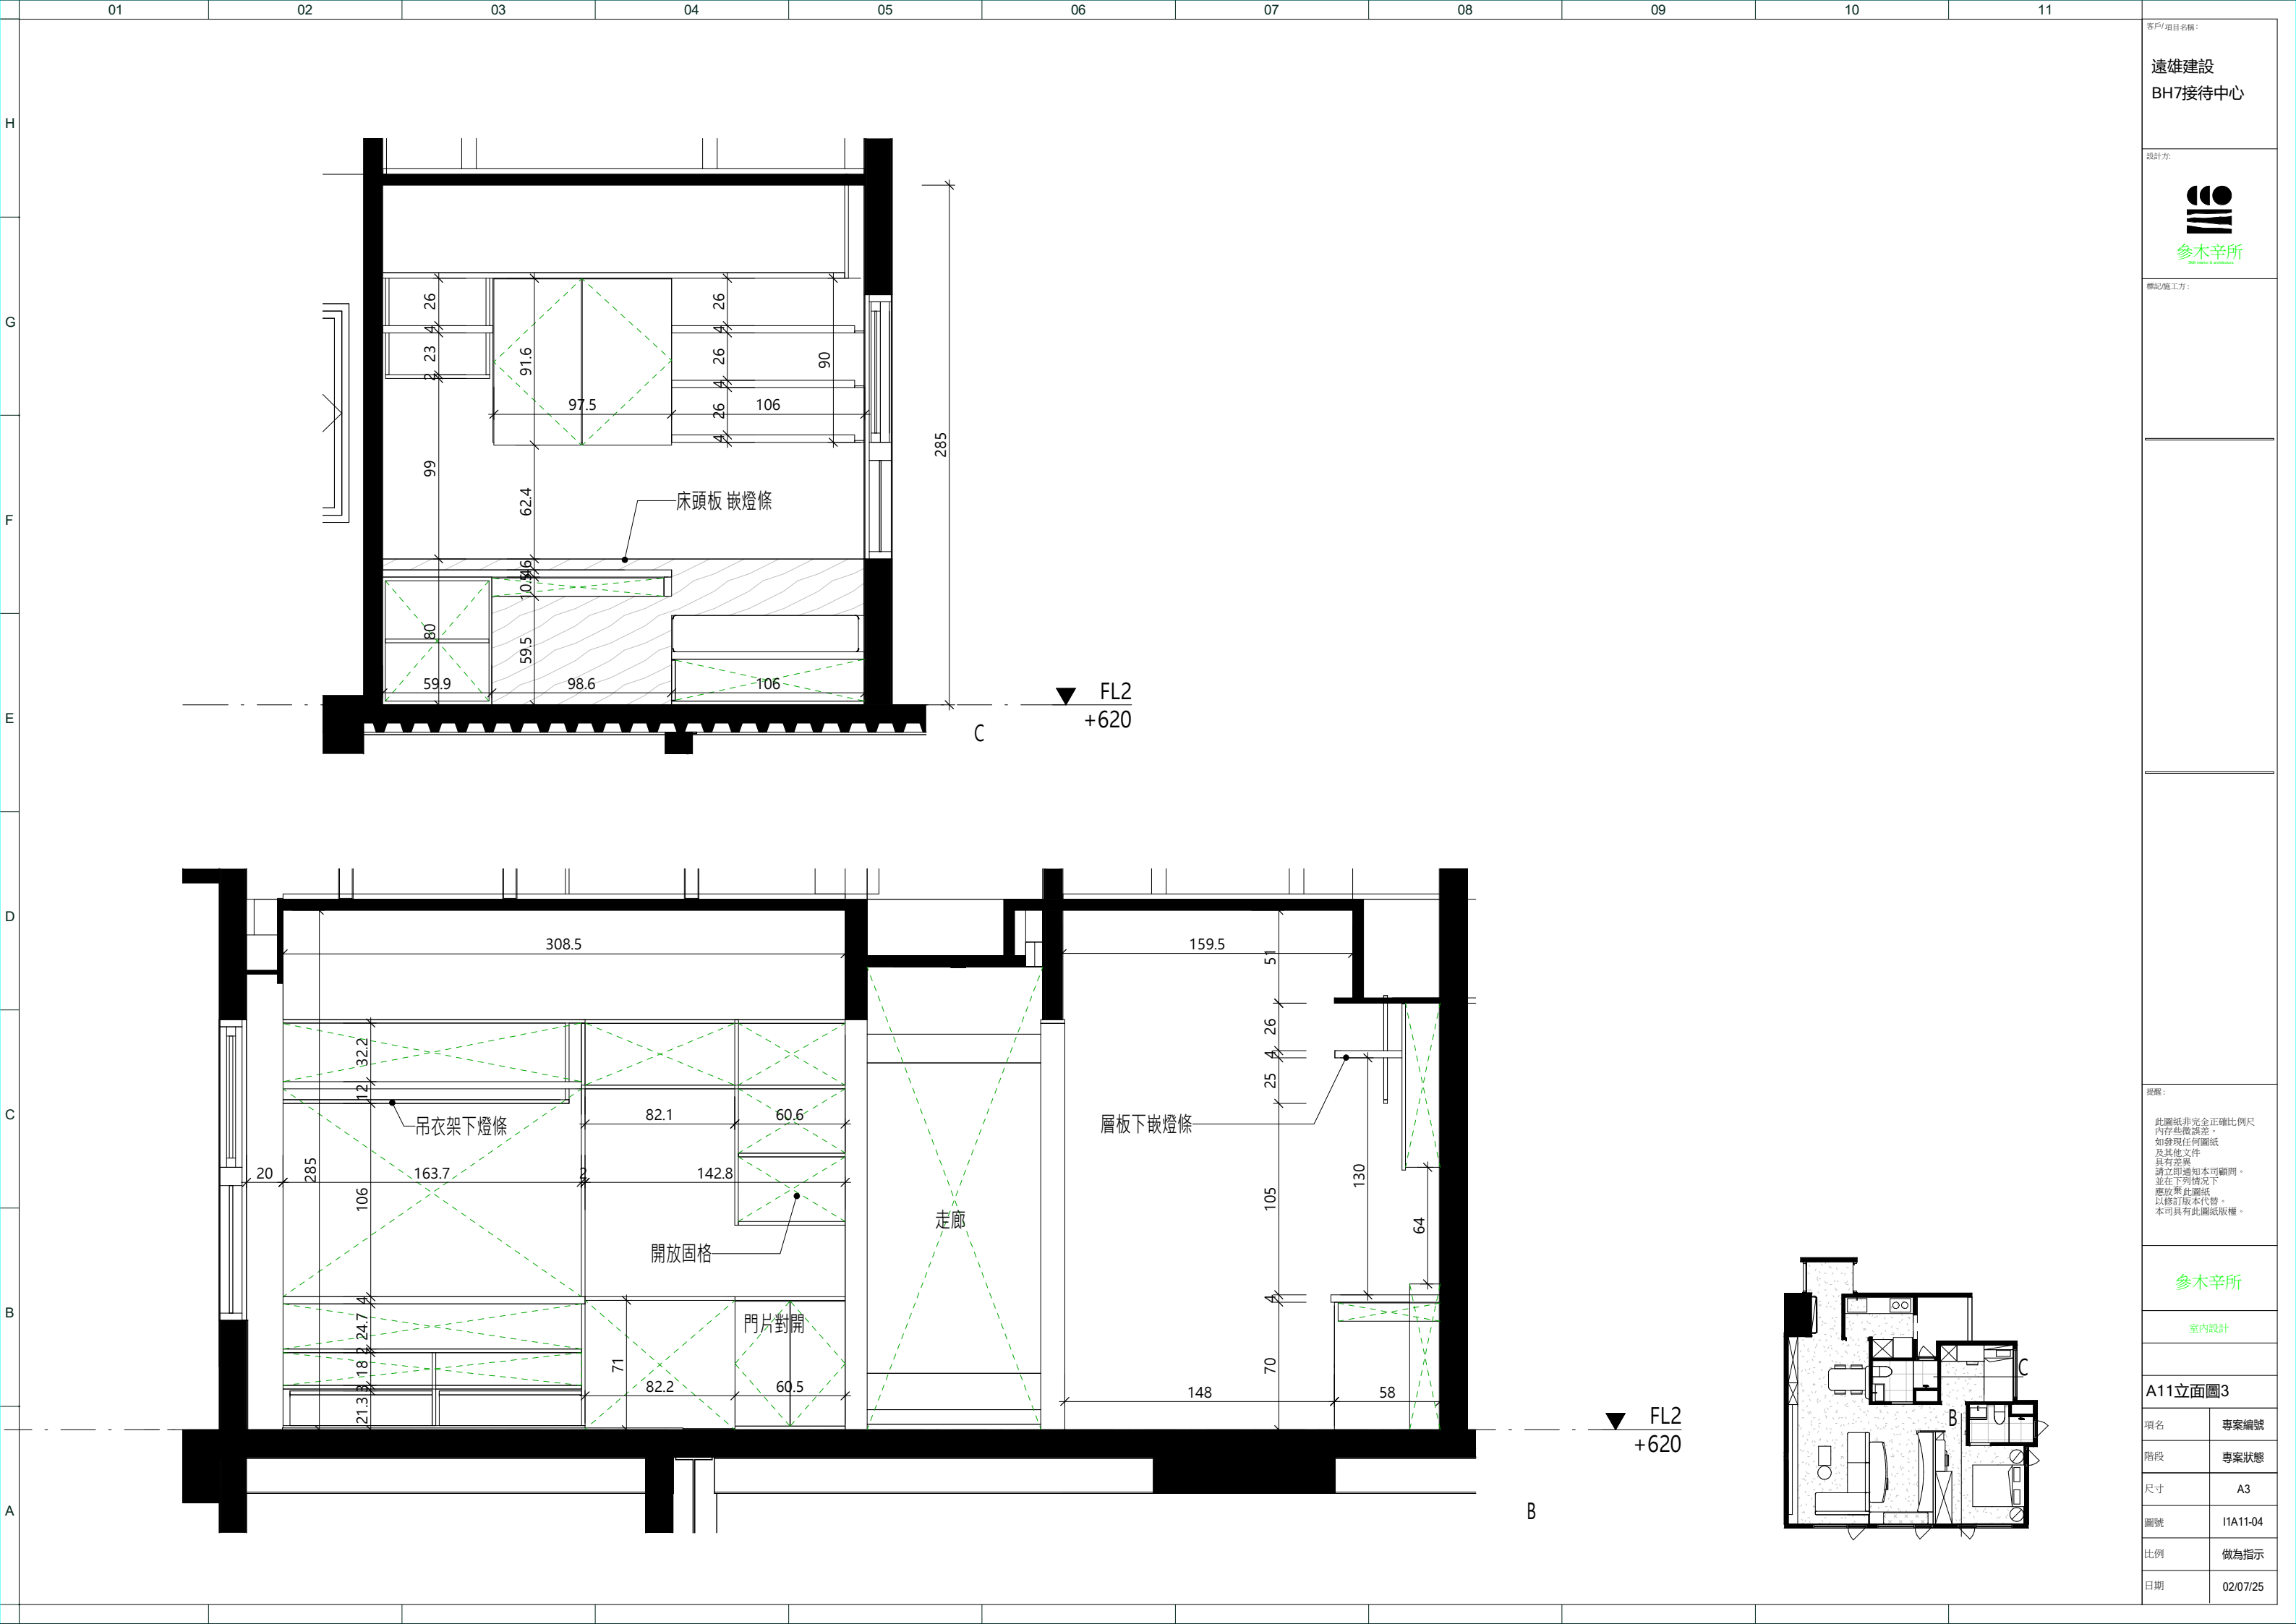

客戶/項目名稱：

遠雄建設
BH7接待中心

設計方：



標記/施工方：

提醒：


此圖紙非完全正確比例尺
內存些微誤差。
如發現任何圖紙
及其他文件
具有差異
請立即通知本司顧問。
並在下列情況下
應放棄此圖紙
以修訂版本代替。
本司具有此圖紙版權。

參木辛所

室內設計

A11立面圖3

項名	專案編號
階段	專案狀態
尺寸	A3
圖號	I1A11-04
比例	做為指示
日期	02/07/25

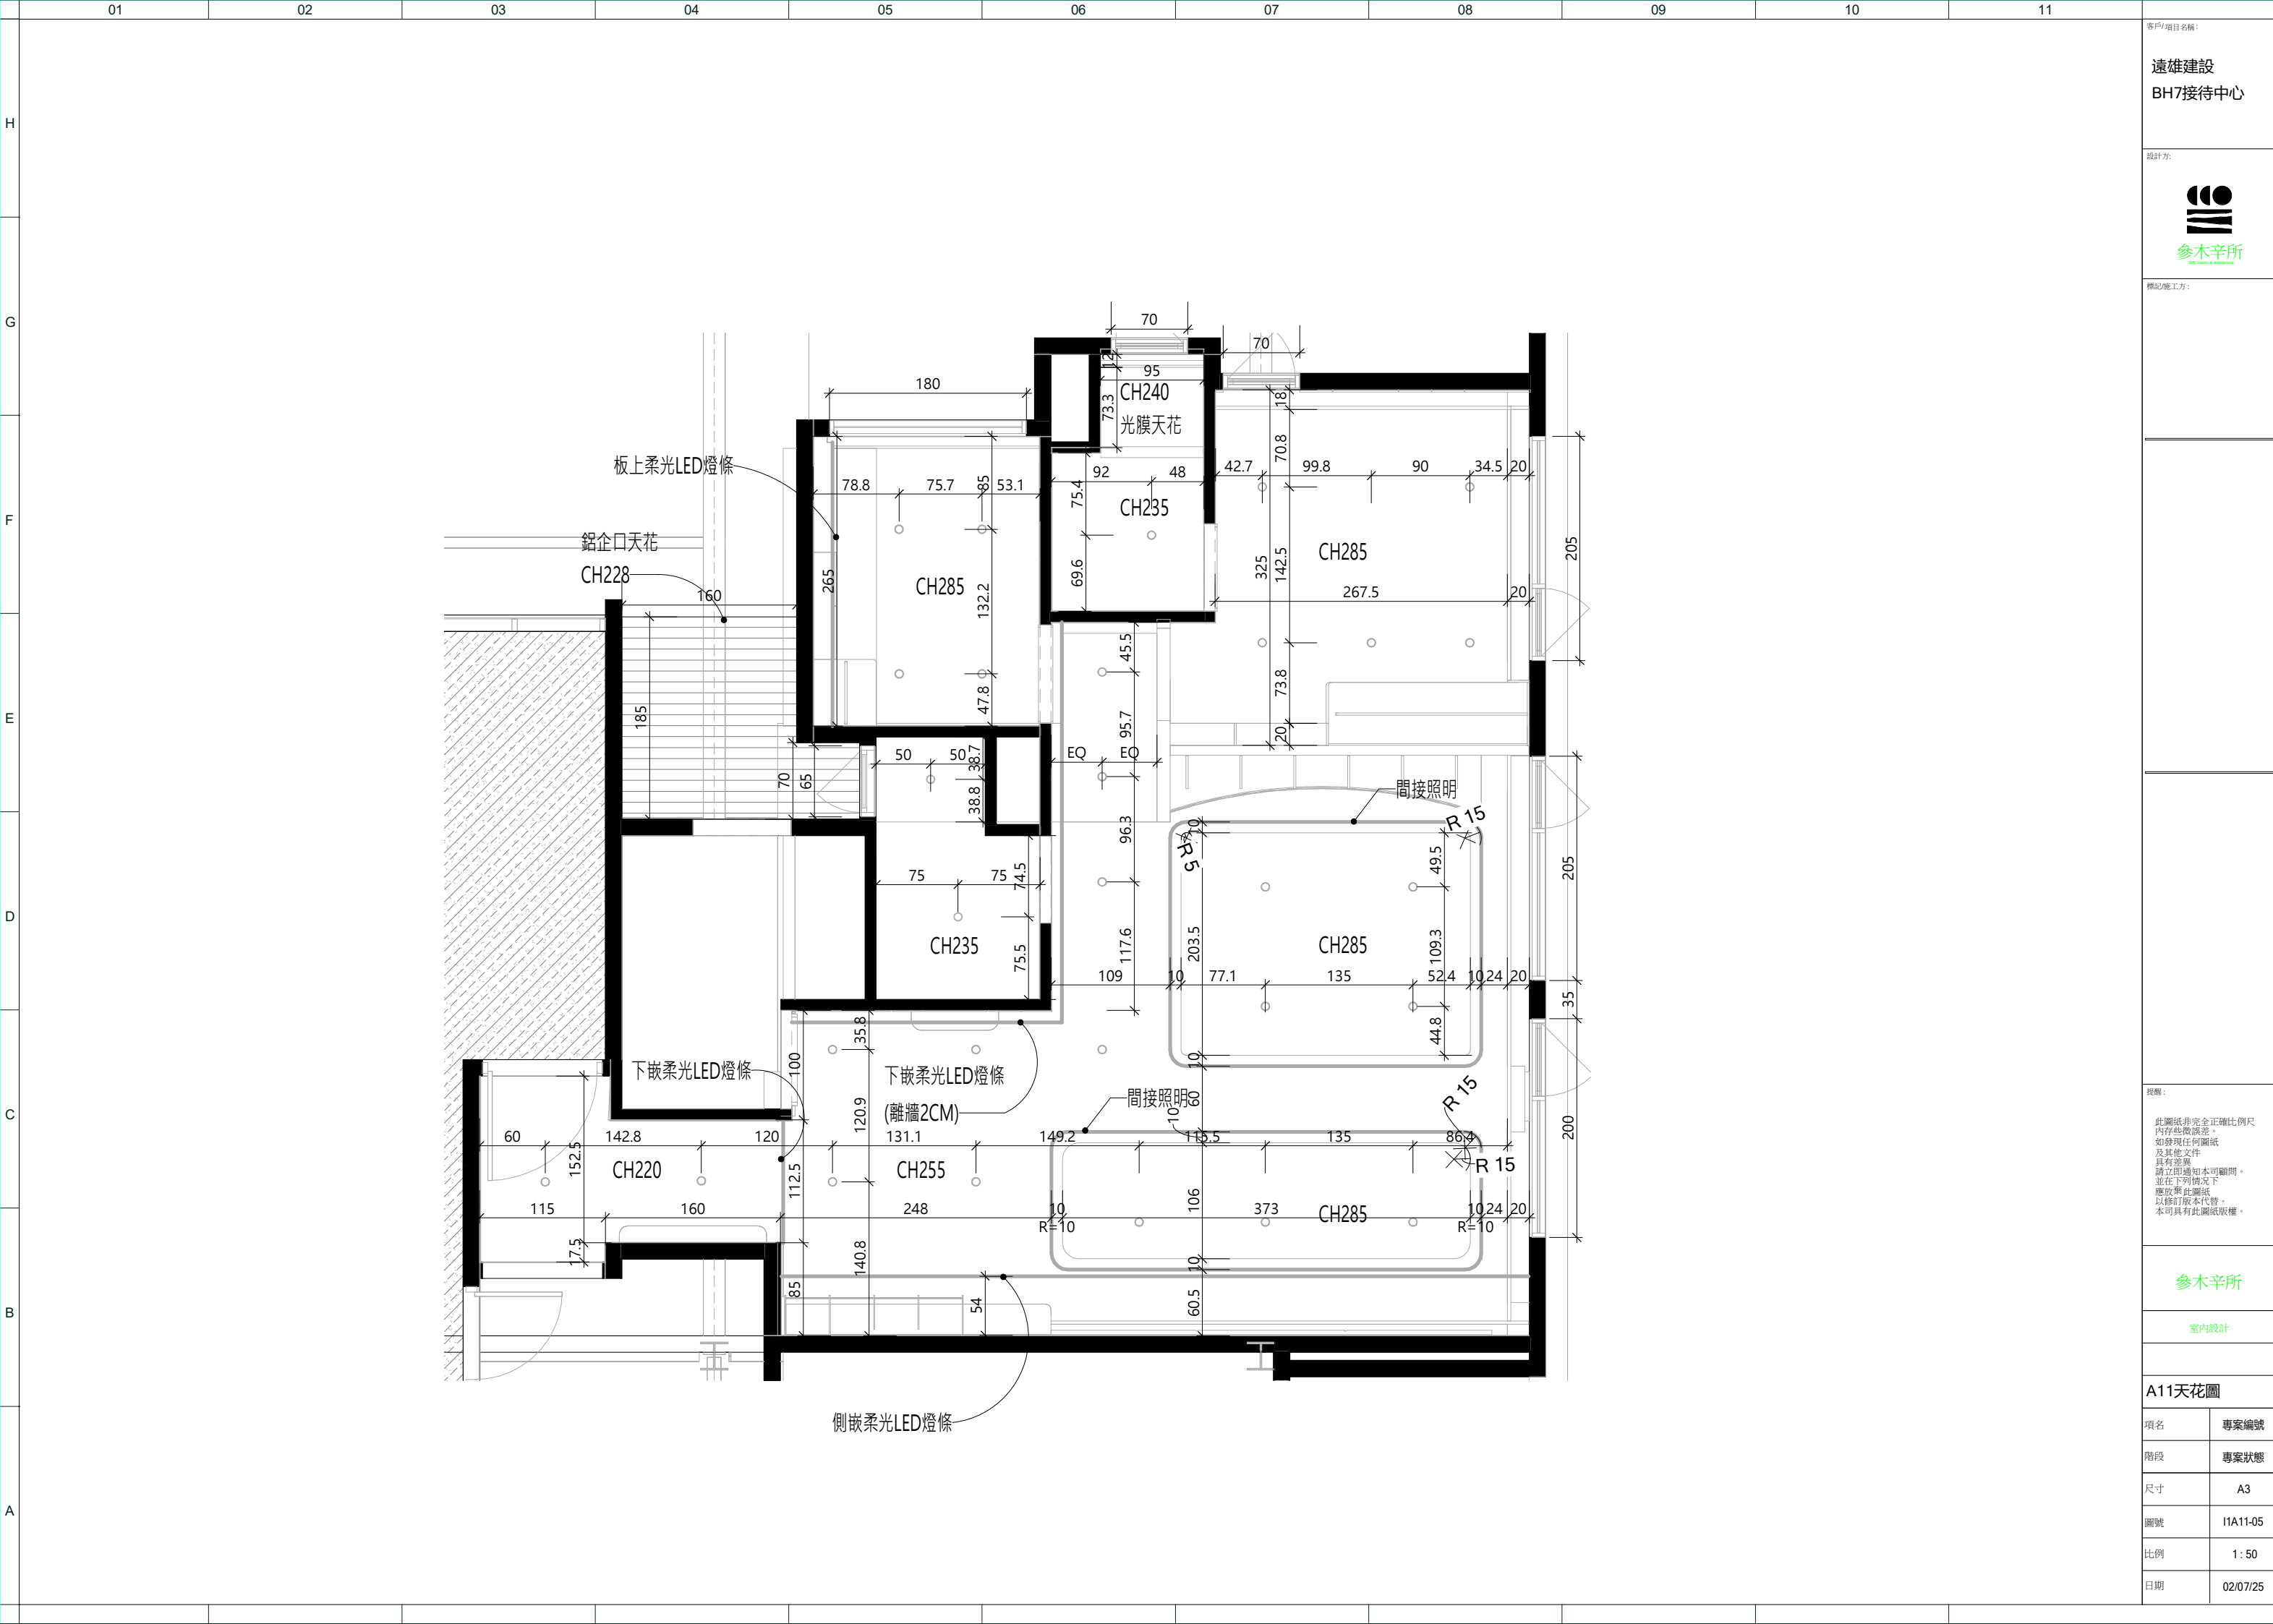

客戶/項目名稱:

遠雄建設
BH7接待中心

設計方:

標記/施工方:

提歷:

此圖紙非完全正確比例尺
內存些微誤差。
如發現任何圖紙
及其他文件
具有差異
請立即通知本司顧問。
並在下列情況下
應放棄此圖紙
以修訂版本代替。
本司具有此圖紙版權。

參木辛所

室內設計

A11天花圖

項名	專案編號
階段	專案狀態
尺寸	A3
圖號	I1A11-05
比例	1 : 50
日期	02/07/25

